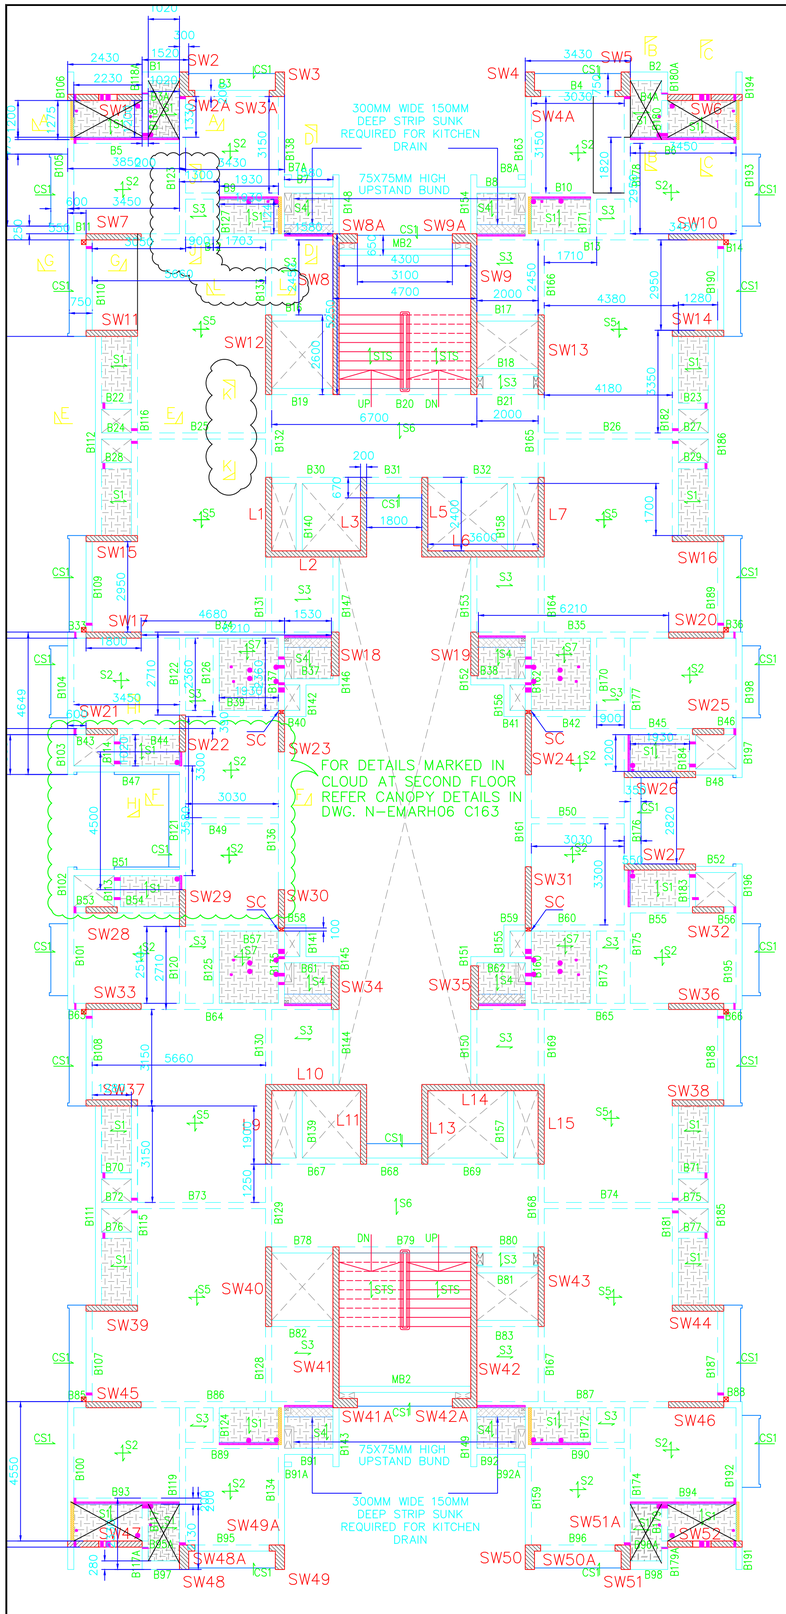

LAYOUT AT SECOND TO FOURTEENTH FLOOR LEVEL

KEY PLAN

Shantigram
THE GOOD LIFE

NOTES:

1. ALL DIMENSIONS ARE IN MILLIMETERS AND LVLS IN METERS UNLESS OTHERWISE SPECIFIED
2. PLEASE DO NOT SCALE THE DRAWING.
3. FOLLOW WRITTEN DIMENSION.
4. ALL DIMENSIONS ARE UNFINISHED DIMENSIONS UNLESS OTHERWISE MENTIONED.
5. DISCREPENCIES SHOULD BE BROUGHT TO THE NOTICE OF ARCHITECT / CONSULTANT.
6. THIS DRAWING IS THE PROPERTY OF ATRECO AND IS NOT TO BE REPRODUCED, COPIED, HANDED OVER TO A THIRD PARTY OR USED FOR ANY PURPOSE OTHER THAN FOR WHICH IT HAS BEEN LOANED.

LEGEND :

REVISIONS

Nos.	Revision Description	Date	Revised By
R00	FOR EXECUTION	08.07.21	S.D.K.
R01	AS PER COMMENTS	22.06.21	S.D.K.
R02	AS PER COMMENTS	03.09.21	S.D.K.
R03	REV. AS PER COMMENTS	30.09.21	S.D.K.
R04	REV. AS PER COMMENTS	19.10.21	S.D.K.
R05	REV. AS PER COMMENTS	16.11.21	S.D.K.

PROJECT:

R-22 PROJECT AT SHANTIGRAM

CLIENT:

adani
Adani Estate Management Private Limited
ATRECO House, CBD, SHANTIGRAM
NR. VAISHNODEVI CIRCLE, S.G.HIGHWAY
AHMEDABAD – 382421 GUJARAT, INDIA

ARCHITECT:

GA design
208 ADHYARU INDUSTRIAL ESTATE, SUNMILL COMPOUND, LOWER PAREL MUMBAI 400013.
TEL: 24980527, 65049256.
email: projects@gadesign.in

MEP CONSULTANTS:

MEPTech
Building Services...Building Confidence...
MEPTECH CONSULTANTS
Address : 904,Supath Building,opp Mc Donald's, 132' Ring Road,Vijay cross Road,Navrangpura, Ahmedabad-380009
Email : info@meptech.in
Web : www.meptech.in
Contact : 079-48011496

LANDSCAPE CONSULTANT:

NEWARCH LANDSCAPES LLP
NEWARCH® LANDSCAPES LLP | +91 22 2833 7173 | +91 22 2898 2904 | 8369102789
202-203, Gokarna, R. M. Bhattad Road, Borivali (W), Mumbai - 400092, INDIA.

EPICONS CONSULTANTS PVT. LTD
ARCHITECTURE AND DETAIL ENGINEERING DIVISION
216 A, Amargain Complex, LBS road, khopat, Thane 400 601
ph 91 22 25471144, 25472356, 25475434 www.epicons.co.in

	Name	Sign
Drawn By	R.A.N	
Checked by	S.D.K	
Approved By	A.S.P	

DWG_NO:
N-EMARH06 C149 R05

DWG_TITLE:
LAYOUT AT SECOND TO FOURTEENTH FLOOR LEVEL

DATE: 16.11.2021

SCALE: 1:100

0 100 200 500 M

N

CAD File No: