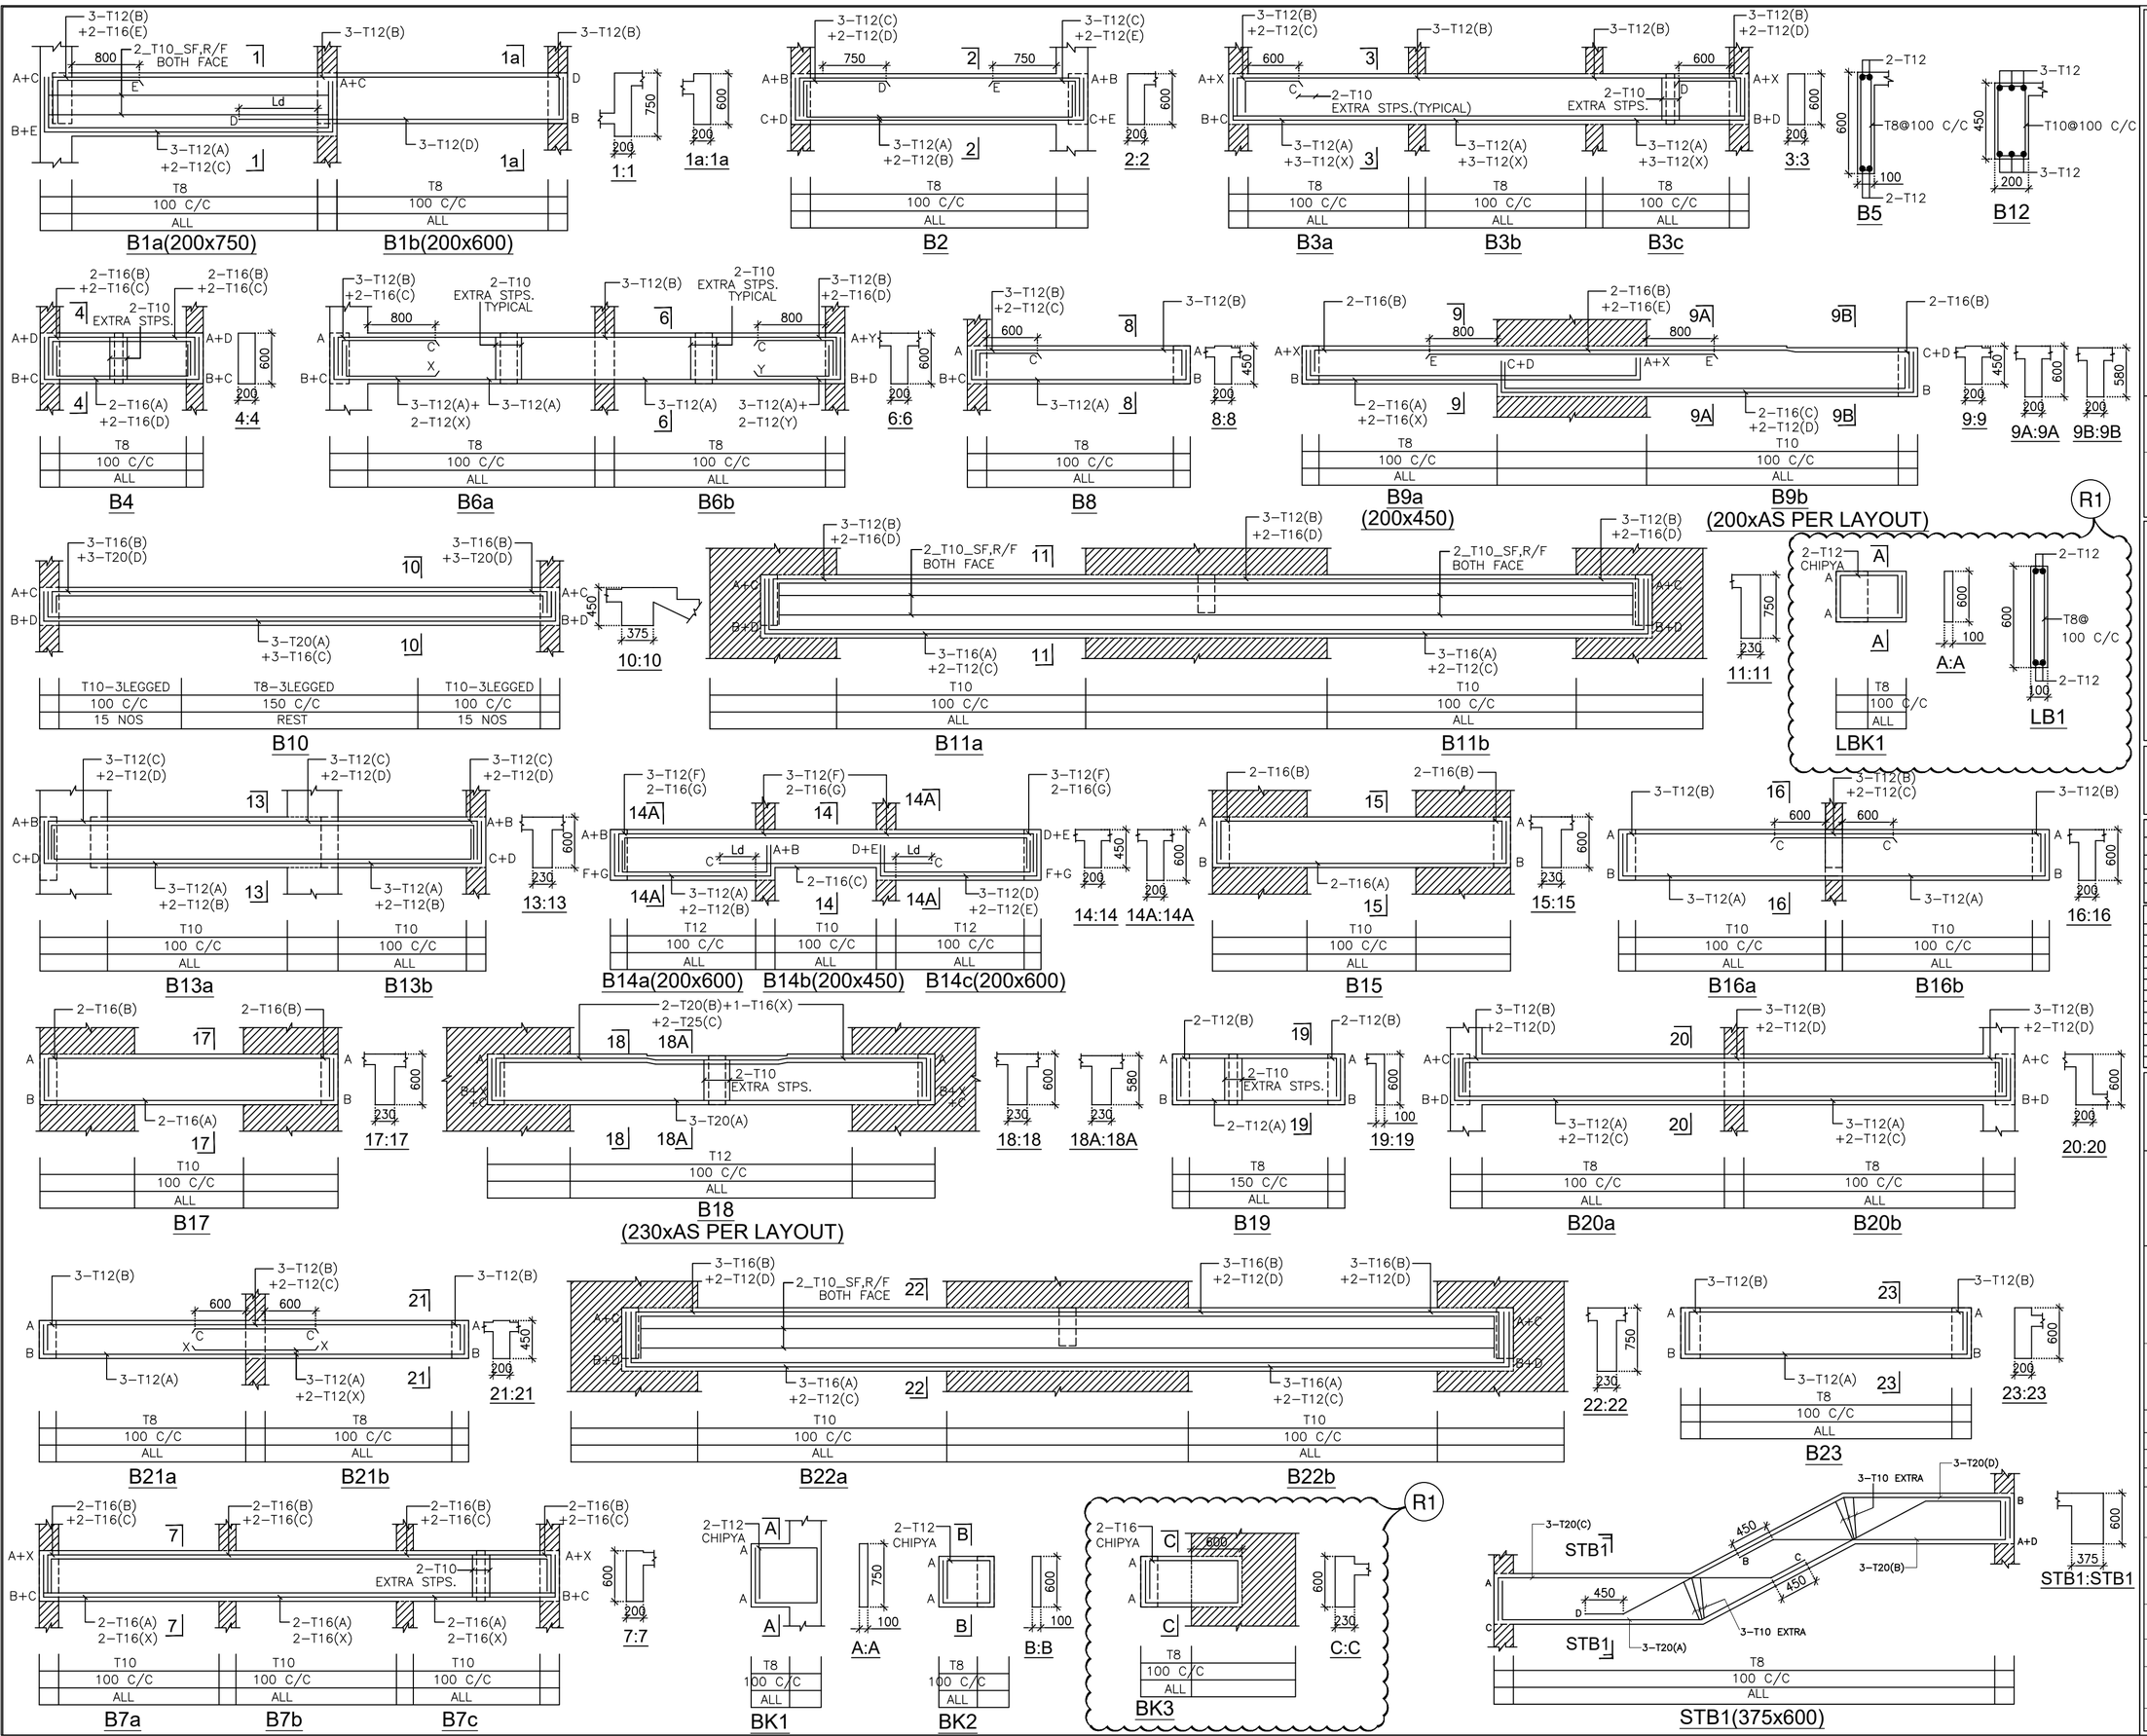

KEY PLAN

Shantigram
THE GOOD LIFE

NOTES:
1. ALL DIMENSIONS ARE IN MILLIMETERS AND LVLS IN MILLIMETERS UNLESS OTHERWISE SPECIFIED
2. FOR ALL NOTES, REFER OUR DRG NO: N-EMARH08 C101

EXCLUSIVE NOTES:

LEGEND :

GOOD FOR CONSTRUCTION
ISSUE ON DATE : 04.02.2021

NO.	DATE	REVISION	BY	DR	CH
R1	04.02.21	REVISED AS PER MARK	DS	J	DS

PRINTS ISSUED

Date	Rev.	Arch	Client	Site	Consl.	Contr.	Office	Total	REMARK
19–03–19	–	MAIL	MAIL+02	–	–	–	01	00	FOR APP
11–06–19	–	MAIL	MAIL	–	–	–	00	00	ADV._G.F.C.
22–06–19	–	MAIL	MAIL	–	–	–	00	00	ADV._G.F.C.
27–08–19	–	MAIL	MAIL	–	–	–	00	00	ADV._G.F.C.
23–09–19	–	MAIL	MAIL+05	–	–	–	00	05	G.F.C.
28–01–20	–	MAIL	MAIL+05	–	–	–	00	05	G.F.C.
04–02–21	R1	MAIL	MAIL	–	–	–	00	00	G.F.C.

ARCHITECT
99 STUDIO
11th. FLOOR, LAND MARK BUILDING, SATELLITE AHMEDABAD
TEL: + 91 079 40028361/62/63
E Mail: info@99studio.in

CONSULTING STRUCTURAL ENGINEER
DUCON CONSULTANTS PVT. LTD.
ADDRESS:A3-A4, 3rd floor, Safal Profitaire, Corporate Road, Opp Prahalad Nagar Garden , SG highway, Ahamdabad.
TEL: +91 -79 -400 73 196
E Mail :- contact@duconconsultants.in

adani
Adani Estate Management Pvt Ltd.
Adani House, Nr. Mithakhali Six Roads, Navrangpura, Ahmedabad, Gujarat, India 38009

PROJECT:
ADANI COMPACT HOUSING

	Name	Sign
Drawn By		
Checked by		
Approved By		

DWG_NO:
N-EMARH08 C531 R1

DWG_TITLE:
STRU. BEAM DETAIL AT TYPICAL FLOOR ROOF SLAB LVL. (TYPE-E,F,I,J,K,L)

DATE :- 15/11/2018

SCALE: 1: 50 / A2

0 100 200 500 M

CAD File No: