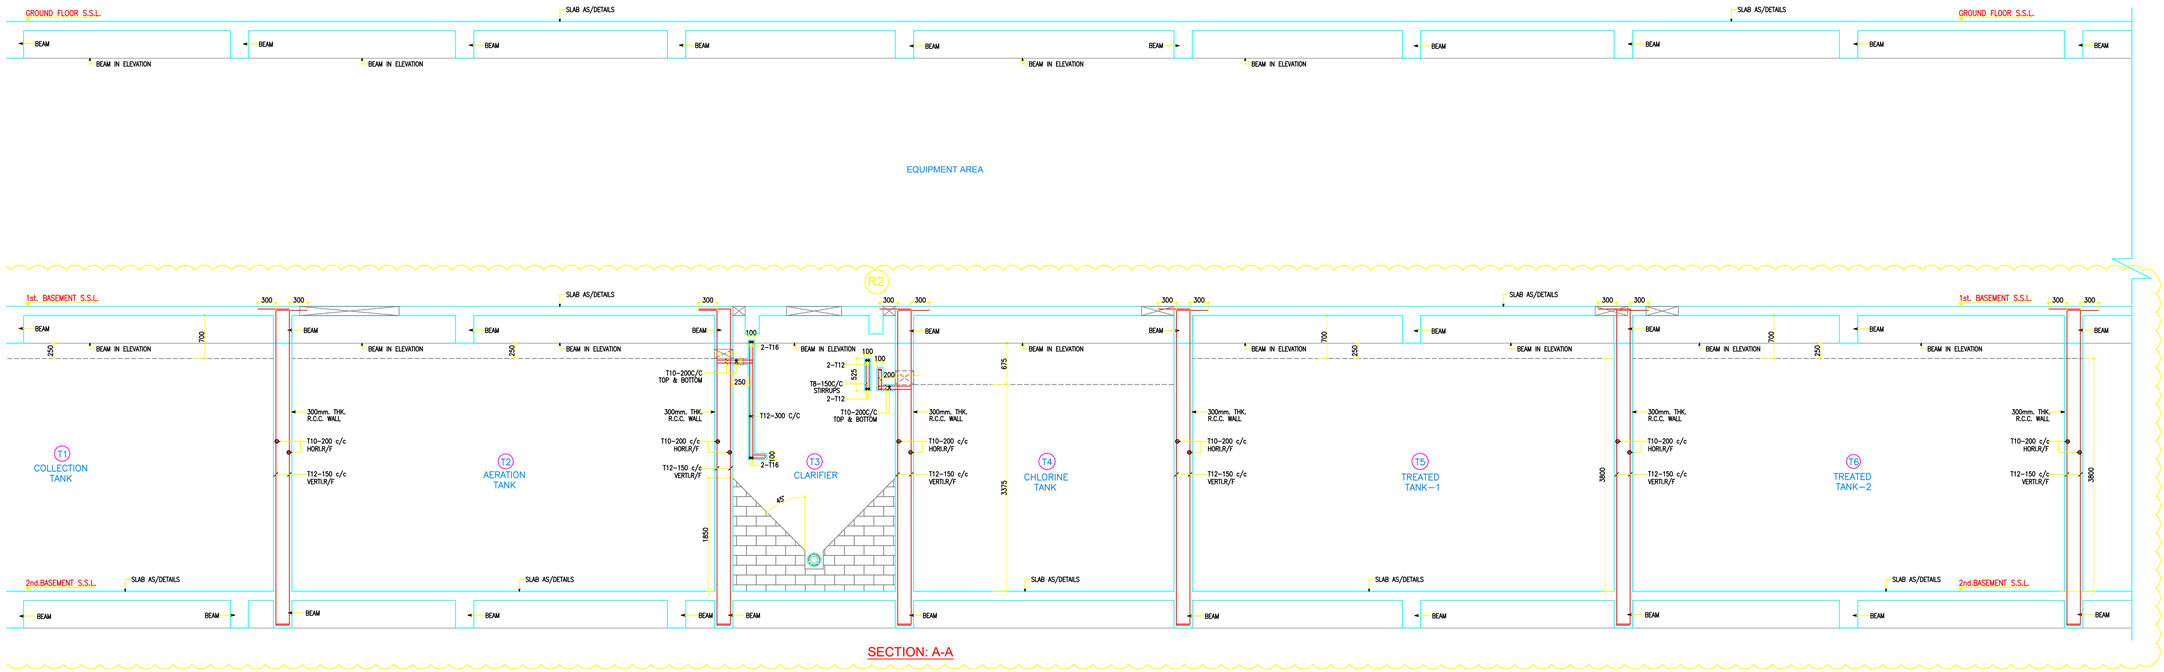

SECTION: A-A

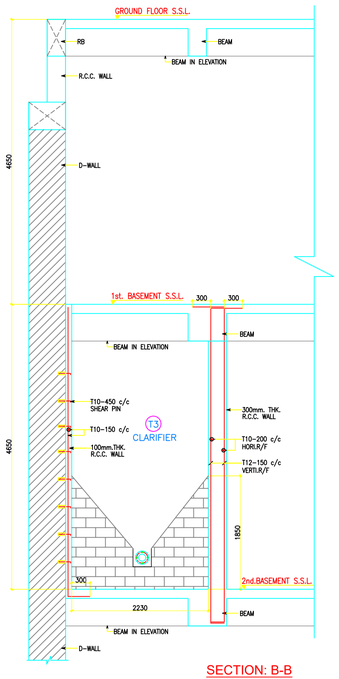

SECTION: B-B

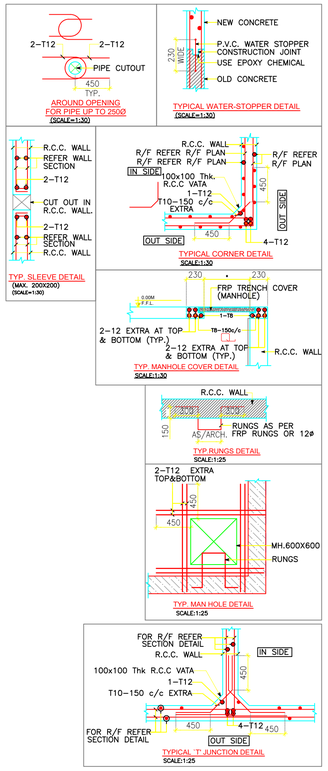

GENERAL NOTES :-

1. ALL DIMENSIONS ARE IN MILLIMETERS AND UNLESS OTHERWISE SPECIFIED.
2. FOR ALL NOTES, REFER OUR DRG NO: STD.01.

GOOD FOR CONSTRUCTION
ISSUED ON DATE-01.11.2023

PRINTS ISSUED

Date	Rev.	Arch	Client	Site	Consl.	Contr.	Office	Total	REMARK
31-05-23	–	MAIL	MAIL	–	–	–	–	–	FOR APPROVAL
24-06-23	–	MAIL	MAIL	MAIL	–	–	01	01	G.F.C.
12-07-23	–	MAIL	MAIL	MAIL+3	–	–	01	04	G.F.C.
15-09-23	R1	MAIL	MAIL	MAIL	–	–	01	01	G.F.C.F.A.
18-09-23	R1	MAIL	MAIL	MAIL	–	–	01	01	G.F.C.
01-11-23	R2	MAIL	MAIL	MAIL+3	–	–	01	04	G.F.C.

NO.	DATE	REVISION	BY	DR	CH
R2	01.11.23	REVISED STP DETAILS	D	B	C
R1	18.09.23	ADDED STP DETAILS	D	B	C

ARCHITECT

VARSHA DESIGN CONSULTANT
B 508 & 509 Gopal Place Opp.ocean Park ,satellite Road,
nehrunagar,ahmedabad
Ph. 74050 00843,92272 26644
E-mail: varshadesign@yahoo.com

JOB TITLE: RESI. APPT. FOR SANGHVI REALTY

DRAWING TITLE: STRUCTURAL SECTIONS DETAILS AT STP. 3rd BASEMENT ROOF SLAB LVL.

JOB NO	DATE	DRG. NO.	REVISION
3922	24-05-22	B3-S-101A	R2

SCALE	SHEET SIZE	DRAWN	DESIGN	CHECKED
1:125	A1	RAVI BABUBHAI	DENISH	CHIRAG

STRUCTURAL CONSULTANT

DUCON
CONSULTANTS PRIVATE LIMITED
A3-A4, 3rd FLOOR, Safal profitaire, Corporate road,
Nr prahladnagar Garden, S.G.ROAD, Ahm'd-51.
E-mail: contact@duconconsultants.in
PH:40073196,29705245,29705246