


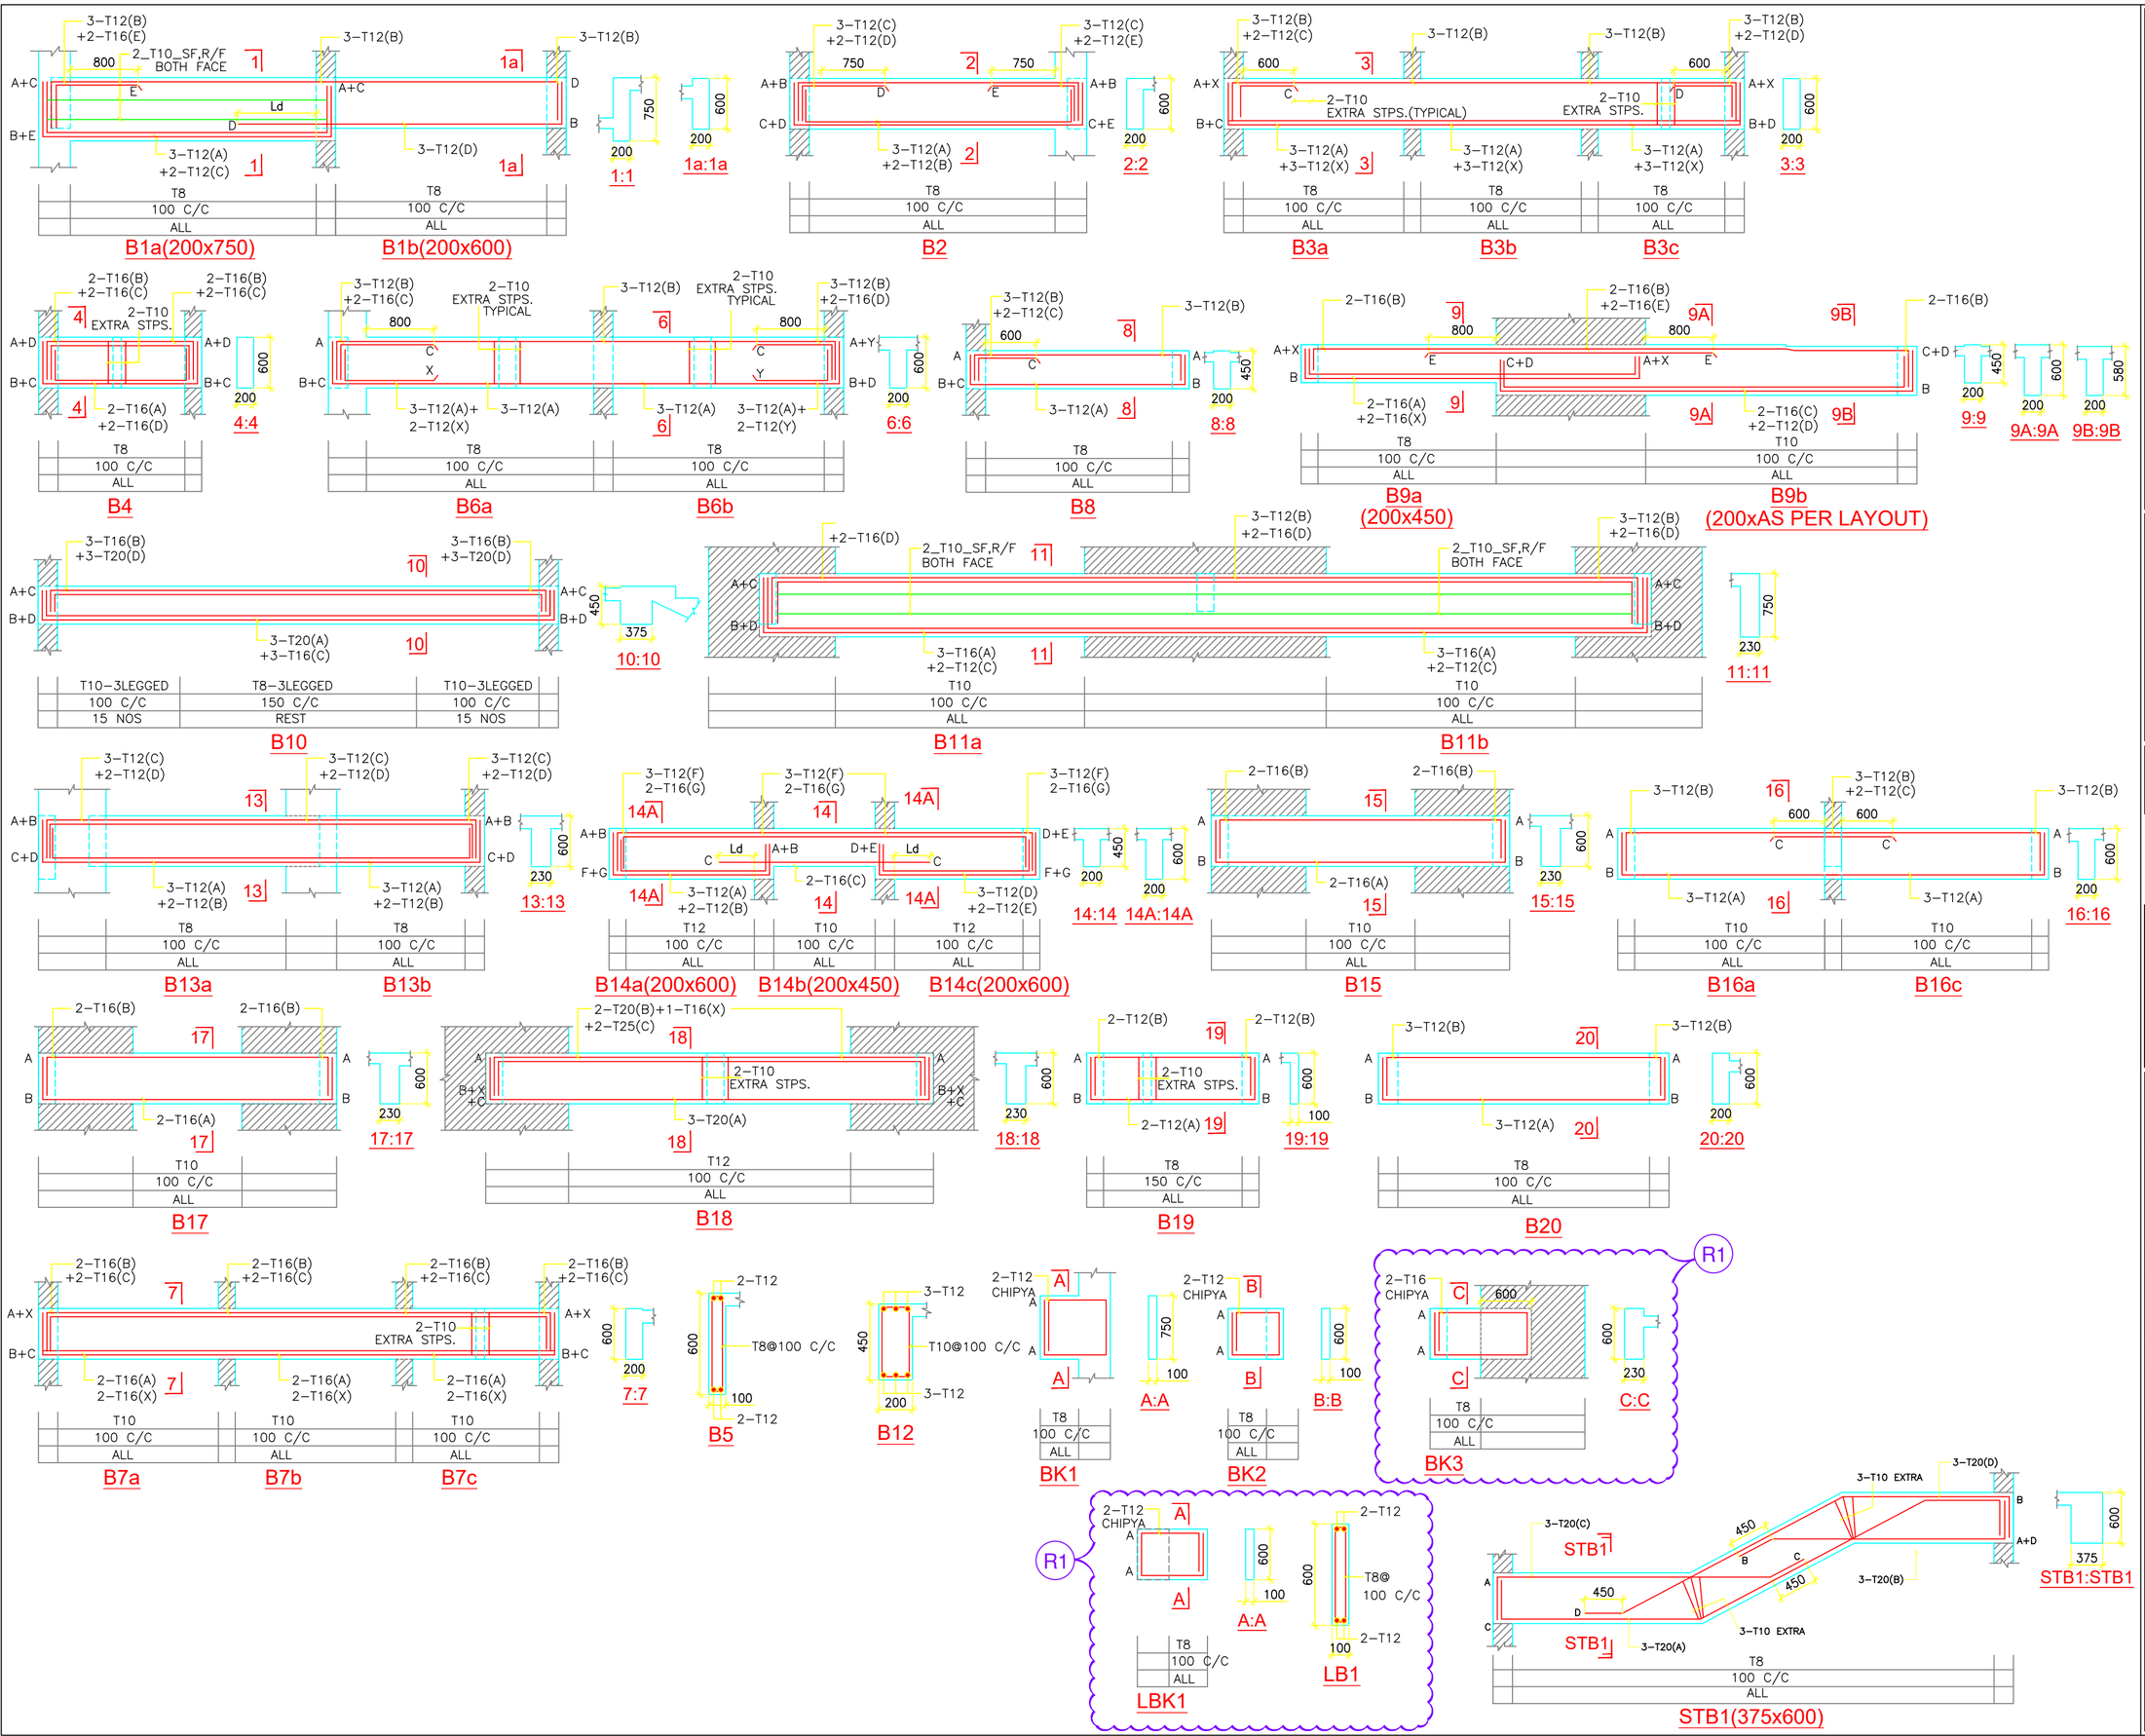


Shantigram
THE GOOD LIFE

NOTES:
1. ALL DIMENSIONS ARE IN MILLIMETERS AND LVLS IN MILLIMETERS UNLESS OTHERWISE SPECIFIED
2. FOR ALL NOTES, REFER OUR DRG NO: N-EMARH08 C101

EXCLUSIVE NOTES:

LEGEND :

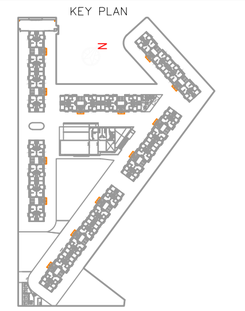GOOD FOR CONSTRUCTION
ISSUE ON DATE : 04.02.2021

| NO. | DATE | REVISION | BY | DR | CH |
|---|---|---|---|---|---|
| R1 | 04.02.21 | REVISED AS PER MARK | DS | J | DS |

PRINTS ISSUED

| Date | Rev. | Arch | Client | Site | Consl. | Contr. | Office | Total | REMARK |
|---|---|---|---|---|---|---|---|---|---|
| 19-03-19 | - | MAIL | MAIL+02 | - | - | - | 01 | 03 | FOR APP |
| 11-06-19 | - | MAIL | MAIL | - | - | - | 00 | 00 | ADV._G.F.C. |
| 22-06-19 | - | MAIL | MAIL | - | - | - | 00 | 00 | ADV._G.F.C. |
| 27-08-19 | - | MAIL | MAIL | - | - | - | 00 | 00 | ADV._G.F.C. |
| 23-09-19 | - | MAIL | MAIL+05 | - | - | - | 00 | 05 | G.F.C. |
| 28-01-20 | - | MAIL | MAIL+05 | - | - | - | 00 | 05 | G.F.C. |
| 04-02-21 | R1 | MAIL | MAIL | - | - | - | 00 | 00 | G.F.C. |


ARCHITECT
**99 STUDIO**
11th. FLOOR, LAND MARK BUILDING, SATELLITE AHMEDABAD
TEL: + 91 079 40028361/62/63
E Mail: info@99studio.in

CONSULTING STRUCTURAL ENGINEER
**DUCON CONSULTANTS PVT. LTD.**
ADDRESS:A3-A4, 3rd floor, Safal Profitaire, Corporate Road, Opp Prahalad Nagar Garden , SG highway, Ahamdabad.
TEL: +91 -79 -400 73 196
E Mail :- contact@duconconsultants.in

adani
Adani Estate Management Pvt Ltd.
Adani House, Nr. Mithakhali Six Roads, Navrangpura, Ahmedabad, Gujarat, India 38009


PROJECT:
ADANI COMPACT HOUSING

| | Name | Sign |
|---|---|---|
| Drawn By | | |
| Checked by | | |
| Approved By | | |

DWG_NO:
N-EMARH08 C551 R1

DWG_TITLE:
STRU. BEAM DETAIL AT TYPICAL FLOOR ROOF SLAB LVL. (TYPE-M)

DATE :- 15/11/2018

SCALE: 1: 50 / A2

0 100 200 500 M

CAD File No: