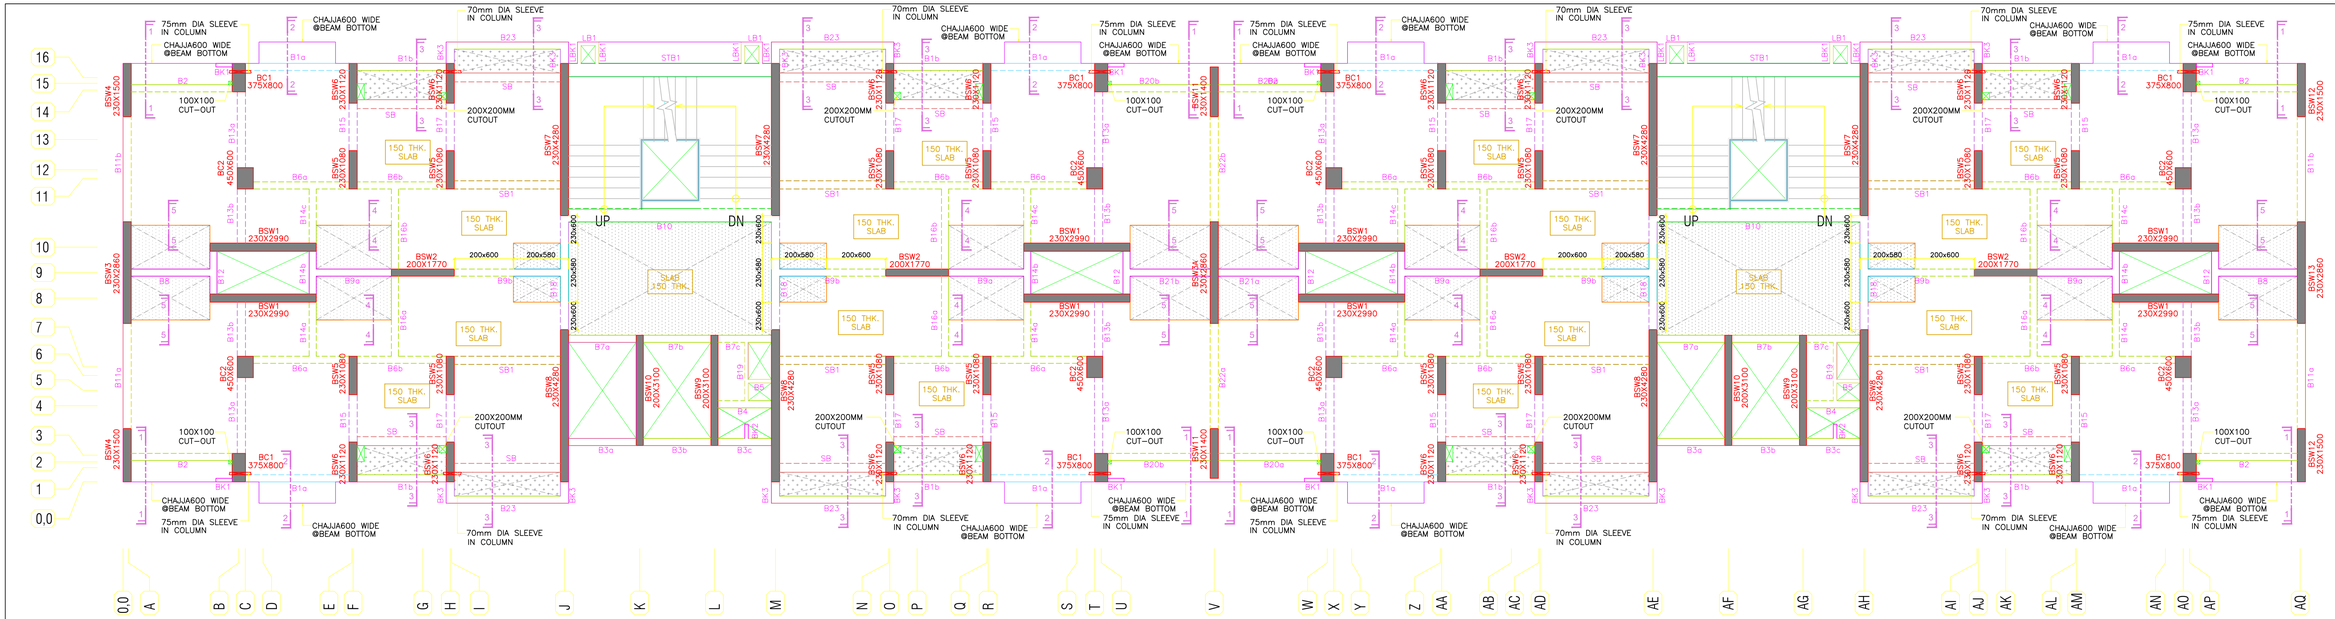

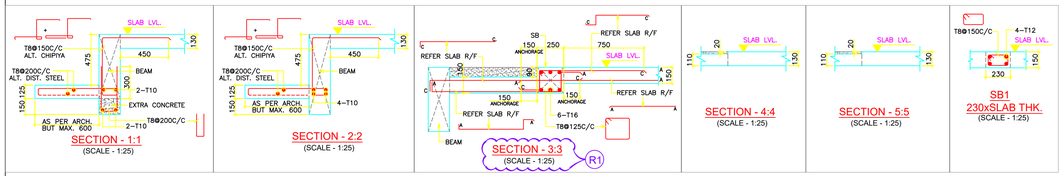

STR. LAY-OUT AT TYP. FLOOR ROOF SLAB LVL. (TYPE-E,F,I,J,K,L)

*FOR ALL CENTRE LINE DIMENSIONS & LOCATION REFER ARCH. DRG.

* ALL SLABS 130THK. R.C.C. SLAB UNLESS OTHERWISE SPECIFIED.

*ALL SUNK SLABS SHALL BE FILLED WITH LIGHT WEIGHT CINDER FILLING - DENSITY NOT MORE THEN THAN 12kn/m³

*ALL MASONRY MUST BE WITH LIGHT WEIGHT AERATED CONC. BLOCK DENSITY NOT MORE THEN 8KN/M³

THUS MARKED CUT-OUT. — THUS MARKED 20mm SUNK SLAB.

THUS MARKED 90mm SUNK SLAB.

SCHEDULE OF BEAM SIZE

BEAM SIZE	BEAM NOS.
200 X 750	B1a,
100 X 600	B5,B13,B2,LB1,LBK1,
230 X 600	B13,B15,B17,BK3,
200 X 600	B1b,B2,B3,B4,B6,B7,B14cc, B16,B20,B23,
375 X 450	B10,
230 X 750	B11,B22
200 X 450	B8,B9a,B12,B14b,B21,
375 X 600	STB1,
100 X 750	BK1,
230 X AS PER LAYOUT	B18
200 X AS PER LAYOUT	B9b

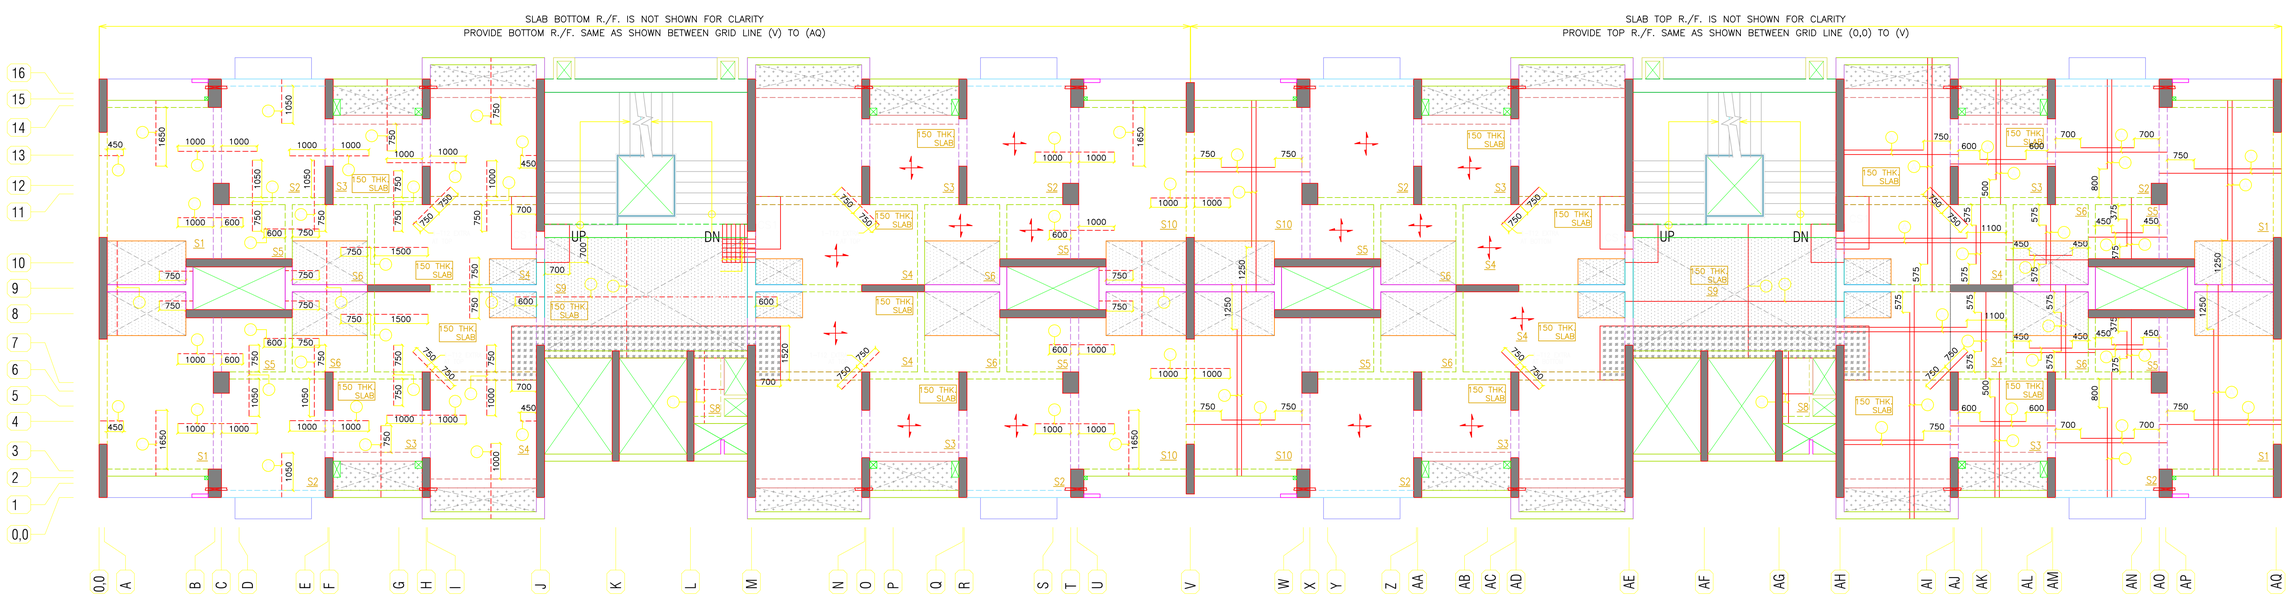

STR. LAY-OUT AT TYP. FLOOR ROOF SLAB LVL. (TYPE-E,F,I,J,K,L)

*FOR ALL CENTRE LINE DIMENSIONS & LOCATION REFER ARCH. DRG.

* ALL SLABS 130THK. R.C.C. SLAB UNLESS OTHERWISE SPECIFIED.

*ALL SUNK SLABS SHALL BE FILLED WITH LIGHT WEIGHT CINDER FILLING - DENSITY NOT MORE THEN THAN 12kn/m³

*ALL MASONRY MUST BE WITH LIGHT WEIGHT AERATED CONC. BLOCK DENSITY NOT MORE THEN 8KN/M³

THUS MARKED CUT-OUT. — THUS MARKED 20mm SUNK SLAB.

THUS MARKED 90mm SUNK SLAB.

THUS MARKED T12-100C/C TOP & BOTTOM EXTRA R/F.

SCHEDULE OF SLAB R/F

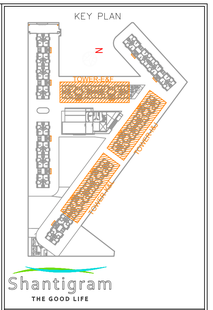

NOTES:
1. ALL DIMENSIONS ARE IN MILLIMETERS AND LVLS IN MILLIMETERS UNLESS OTHERWISE SPECIFIED
2. FOR ALL NOTES, REFER OUR DRG NO: N-EMARH08 C101

EXCLUSIVE NOTES:

LEGEND :

GOOD FOR CONSTRUCTION
ISSUE ON DATE : 04.02.2021

NO.	DATE	REVISION	BY	DR	CH
R1	04.02.21	REVISED AS PER MARK	DS	J	DS

PRINTS ISSUED

Date	Rev	Arch.	Client	Site	Consul.	Contr.	Office	Total	REMR
19-03-19	-	MAL	MAL+02	-	-	-	01	03	FOR APP
08-04-19	-	MAL	MAL	-	-	-	00	00	FOR APP
11-06-19	-	MAL	MAL	-	-	-	00	00	ADN_EFG
22-06-19	-	MAL	MAL	-	-	-	00	00	ADN_EFG
24-07-19	-	MAL	MAL	-	-	-	00	00	FOR APP
27-08-19	-	MAL	MAL	-	-	-	00	00	ADN_EFG
23-09-19	-	MAL	MAL+05	-	-	-	00	05	EFG
28-01-20	-	MAL	MAL+05	-	-	-	00	05	EFG
04-02-21	R1	MAL	MAL	-	-	-	00	00	EFG

ARCHITECT
99 STUDIO
1TH. FLOOR, LAND MARK BUILDING, SATELLITE AHMEDABAD
TEL: + 91 079 40028361/62/63
E Mail: info@99studio.in

CONSULTING STRUCTURAL ENGINEER
DUCON CONSULTANTS PVT. LTD.
ADDRESS:A3-A4, 3rd floor, Safal Profitaire, Corporate Road, Opp Prahalad Nagar Garden , SG highway, Ahamdabad.
TEL : +91 -79 -400 73 196
E Mail :- contact@duconconsultants.in

adani
Adani Estate Management Pvt Ltd.
Adani House, Nr. Mithakhali Six Roads, Navrangpura, Ahmedabad, Gujarat, India 380009

PROJECT:
ADANI COMPACT HOUSING

	Name	Sign
Drawn By		
Checked by		
Approved By		

DWG_NO:
N-EMARH08 C521 R1

DWG_TITLE:
STR. LAY-OUT AT TYP. FLOOR ROOF SLAB LVL. (TYPE-E,F,I,J,K,L)

DATE :- 15/11/2018

SCALE: 1: 75

0 100 200 500 M

CAD File No: