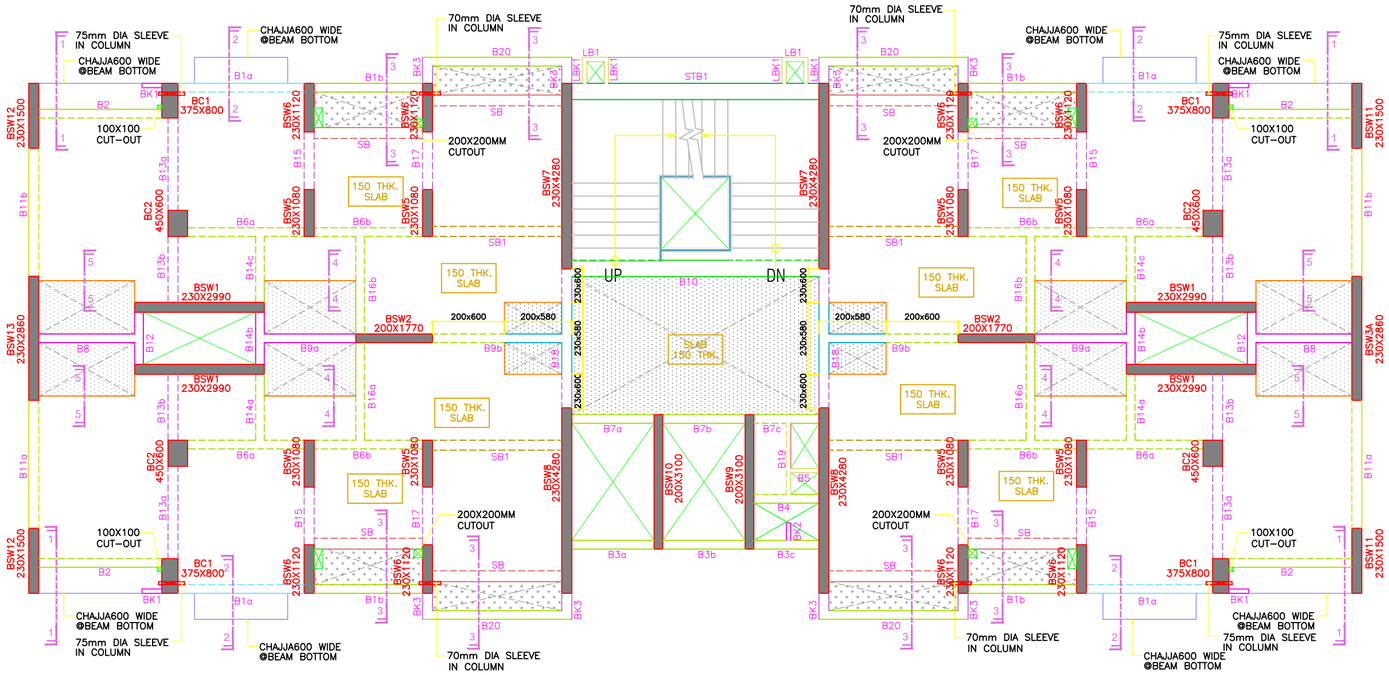

STR. LAY-OUT AT TYP. FLOOR ROOF SLAB LVL. (TYPE-M)

*FOR ALL CENTRE LINE DIMENSIONS & LOCATION REFER ARCH. DRG.

* ALL SLABS 130THK. R.C.C. SLAB UNLESS OTHERWISE SPECIFIED.

*ALL SUNK SLABS SHALL BE FILLED WITH LIGHT WEIGHT CINDER FILLING - DENSITY NOT MORE THEN THAN 12kn/m³

*ALL MASONRY MUST BE WITH LIGHT WEIGHT AERATED CONC. BLOCK DENSITY NOT MORE THEN 8KN/M³

THUS MARKED CUT-OUT. — THUS MARKED 20mm SUNK SLAB.

THUS MARKED 90mm SUNK SLAB.

SLAB BOTTOM R./F. IS NOT SHOWN FOR CLARITY
PROVIDE BOTTOM R./F. SAME AS SHOWN AT OPPOSITE SIDE

SLAB TOP R./F. IS NOT SHOWN FOR CLARITY
PROVIDE TOP R./F. SAME AS SHOWN AT OPPOSITE SIDE

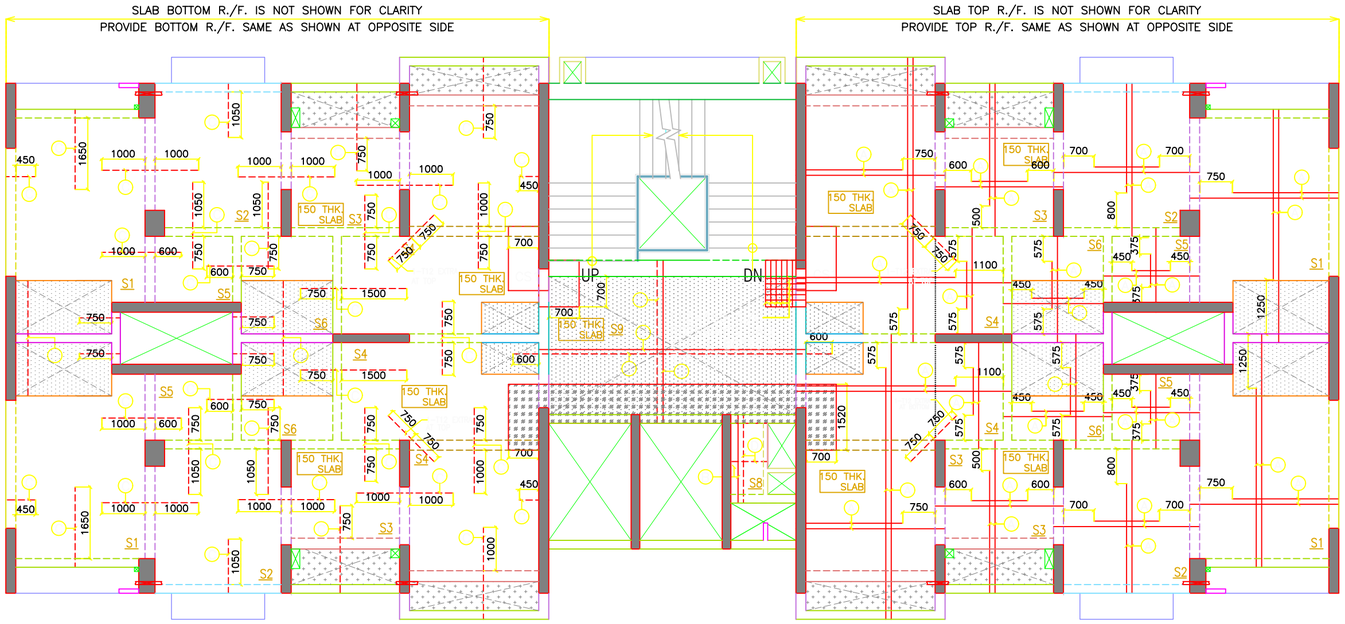

STR. LAY-OUT AT TYP. FLOOR ROOF SLAB LVL. (TYPE-M)

*FOR ALL CENTRE LINE DIMENSIONS & LOCATION REFER ARCH. DRG.

* ALL SLABS 130THK. R.C.C. SLAB UNLESS OTHERWISE SPECIFIED.

*ALL SUNK SLABS SHALL BE FILLED WITH LIGHT WEIGHT CINDER FILLING - DENSITY NOT MORE THEN THAN 12kn/m³

*ALL MASONRY MUST BE WITH LIGHT WEIGHT AERATED CONC. BLOCK DENSITY NOT MORE THEN 8KN/M³

THUS MARKED CUT-OUT. — THUS MARKED 20mm SUNK SLAB.

THUS MARKED 90mm SUNK SLAB. — THUS MARKED T12-100C/C TOP & BOTTOM EXTRA R/F.

SCHEDULE OF BEAM SIZE

BEAM SIZE	BEAM NOS.
200 X 750	B1a,
100 X 600	B5,B19,BK2,LB1,LBK1,
230 X 600	B13,B15,B17,BK3,
200 X 600	B1b,B2,B3,B4,B6,B7,B14ac,B16, B20,
375 X 450	B10,
230 X 750	B11,
200 X 450	B8,B9a,B12,B14b,
375 X 600	STB1,
100 X 750	BK1,
AS PER LAYOUT	B18
AS PER LAYOUT	B9b

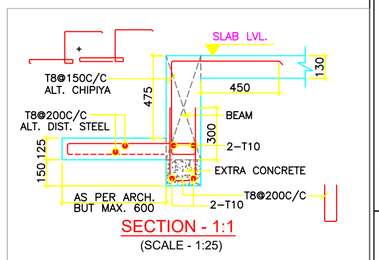

SECTION - 1:1
(SCALE - 1:25)

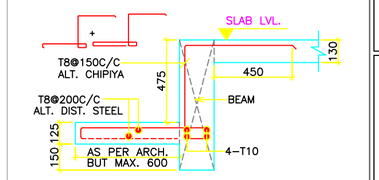

SECTION - 2:2
(SCALE - 1:25)

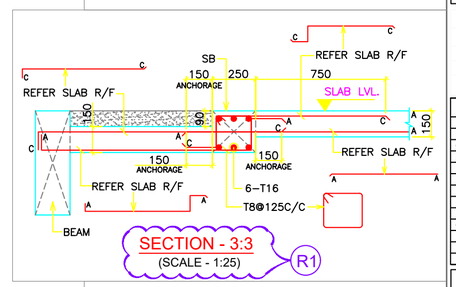

SECTION - 3:3
(SCALE - 1:25)

R1

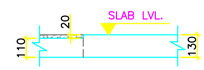

SECTION - 4:4
(SCALE - 1:25)

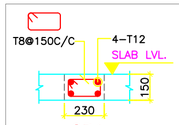

SB1
230xSLAB THK.
(SCALE - 1:25)

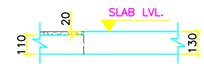

SECTION - 5:5
(SCALE - 1:25)

SCHEDULE OF SLAB R/F

KEY PLAN

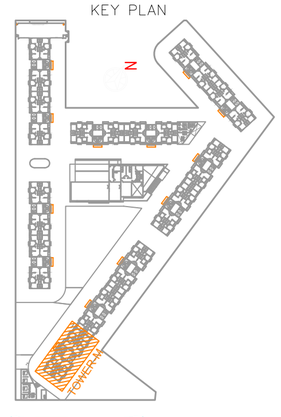

Shantigram
THE GOOD LIFE

NOTES:
1. ALL DIMENSIONS ARE IN MILLIMETERS AND LVLS IN MILLIMETERS UNLESS OTHERWISE SPECIFIED
2. FOR ALL NOTES, REFER OUR DRG NO: N-EMARH08 C101

EXCLUSIVE NOTES:

LEGEND :

GOOD FOR CONSTRUCTION
ISSUE ON DATE : 04.02.2021

NO.	DATE	REVISION	BY	DR	CH
R1	04.02.21	REVISED AS PER MARK	DS	J	DS

PRINTS ISSUED

Date	Rev.	Arch	Client	Site	Consl.	Contr.	Office	Total	REMARK
19-03-19	-	MAIL	MAIL+02	-	-	-	01	03	FOR APP.
09-04-19	-	MAIL	MAIL	-	-	-	00	00	FOR APP.
11-06-19	-	MAIL	MAIL	-	-	-	00	00	ADV._G.F.C.
22-06-19	-	MAIL	MAIL	-	-	-	00	00	ADV._G.F.C.
24-07-19	-	MAIL	MAIL	-	-	-	00	00	FOR APP.
27-08-19	-	MAIL	MAIL	-	-	-	00	00	ADV._G.F.C.
23-09-19	-	MAIL	MAIL+05	-	-	-	00	05	G.F.C.
28-01-20	-	MAIL	MAIL+05	-	-	-	00	05	G.F.C.
04-02-21	R1	MAIL	MAIL	-	-	-	00	00	G.F.C.

ARCHITECT
99 STUDIO
11th. FLOOR, LAND MARK BUILDING, SATELLITE AHMEDABAD
TEL: + 91 079 40028361/62/63
E Mail: info@99studio.in

CONSULTING STRUCTURAL ENGINEER
DUCON CONSULTANTS PVT. LTD.
ADDRESS:A3-A4, 3rd floor, Safal Profitaire, Corporate Road, Opp Prahalad Nagar Garden , SG highway, Ahamdabad.
TEL: +91 -79 -400 73 196
E Mail :- contact@duconconsultants.in

adani
Adani Estate Management Pvt Ltd.
Adani House, Nr. Mithakhali Six Roads, Navrangpura, Ahmedabad, Gujarat, India 38009

PROJECT:
ADANI COMPACT HOUSING

	Name	Sign
Drawn By		
Checked by		
Approved By		

DWG_NO:
N-EMARH08 C541 R1

DWG_TITLE:
STR. LAY-OUT AT TYP. FLOOR ROOF SLAB LVL. (TYPE - M)

DATE :- 15/11/2018

SCALE: 1: 100 / A2

0 100 200 500 M

CAD File No: