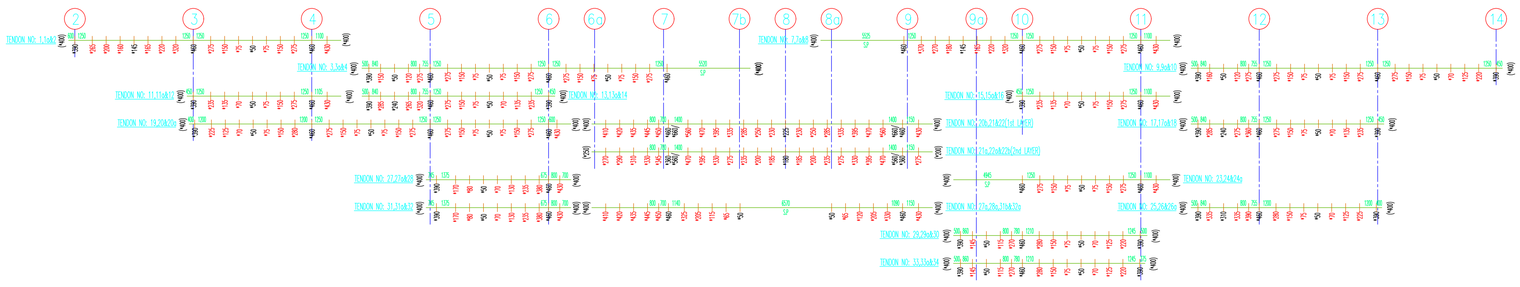

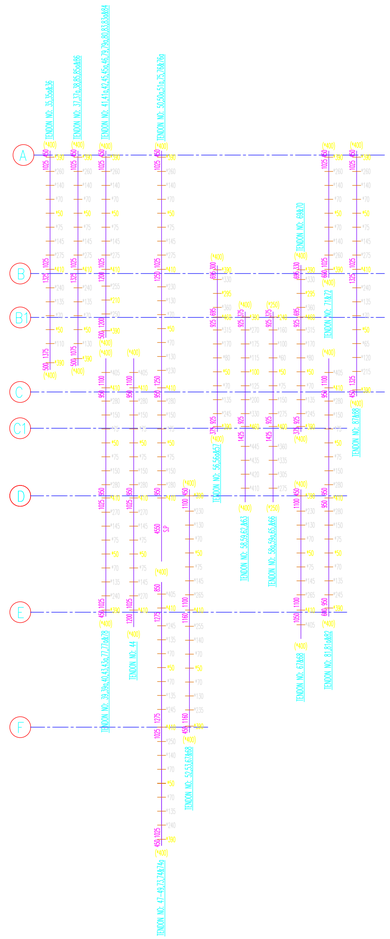

3RD FLOOR PT BEAM TENDON PROFILES (POST-TENSIONED)

Scale = 1:150

NOTES:
UNLESS OTHERWISE SHOWN.
1) USE 0.5" OR 12.7mm STRAND.
2) ALL TENDON PROFILE SPACING NOT SHOWN TO BE 1000.
3) ALL TENDON SPLAY SHOULD BE 1 IN 10 & 1 IN 8 SLOPE.
4) ( ) DENOTES TENDON PROFILE MEASURED FROM SOFFIT OF BEAM TO C.G. OF DUCTS.
5) DEAD END & LIVE END CAN BE INTERCHANGED AS PER SITE CONDITION FOR STRESSING FEASIBILITY.
6) * DENOTES TENDON PROFILE MEASURED FROM SOFFIT OF PT BEAM
7) 'V' DENOTES VARIES.
8) SP - DENOTES STRAIGHT RPOFILES
9) TENDON NO: 5,6,54,55,60,61&64NOT IN USE.

GOOD FOR CONSTRUCTION

GR0	BASED ON COORDINATION DWG REV-R1	PRATHIP	KAUSHIK	KRISHNA
		23-05-23	SEELAM	RVR
Rev.	Description	Drawn	Designed	Checked
		Date	Approved	Reviewed

ARCHITECT:
M/S.ARCOP ASSOCIATES

CLIENT:
M/S.GLOBAL HEALTH CITY PVT LTD

CONSULTANT:
TPC TECHNICAL PROJECTS CONSULTANTS(P)LTD.
H.O:- B-74, SECTOR 57, NOIDA
UTTAR PRADESH-201301(INDIA)
BOARD NO:-91-120-4308800

PT SPECIALIST:
UTRACON STRUCTURAL SYSTEMS PVT LTD
No.45, 5th Street,Padmanaba Nagar, Adyar,
Chennai-600 020, INDIA
Tel:+91 (44) 24468001/2/3 Fax:+91 (44) 2446 8004
E-Mail: utraconindia@utracon.com
Website: www.utraconindia.com

PROJECT TITLE:
PROPOSED BUILDING FOR MEDANTA HOSPITAL AT NOIDA,UP.

DRAWING TITLE:
POST-TENSIONED
3RD FLOOR LAYOUT
PT BEAM TENDON PROFILES

DRAWN:	DESIGNED:	CHECKED:	REVIEWED:
V.VINOTH	KAUSHIK	KRISHNA	RVR
SCALE:	DATE:	E-MAIL:	APPROVED:
1:150	28-04-23	ussdesign1@utraconindia.com	SEELAM

DRAWING NO: 220517/SD/3-P1
REVISION: GR0

ongoing\delhi\2022\220517-proposed building for medanta hospital at noida\pdsgning\3rd floor

THIS DRAWING IS COPYRIGHT AND REMAINS THE PROPERTY OF UTRACON STRUCTURAL SYSTEMS PVT LTD AND MUST NOT BE USED/RETAINED OR COPIED WITHOUT WRITTEN PERMISSION.

ORIGINAL SIZE OF THIS DRAWING IS A0