THIS DRAWING IS THE PROPERTY OF DELF INDIA & SHALL NOT BE COPIED OR REPRODUCED EITHER WHOLLY OR IN PART WITHOUT THE WRITTEN PERMISSION OF THE AFORMENTIONED COMPANY

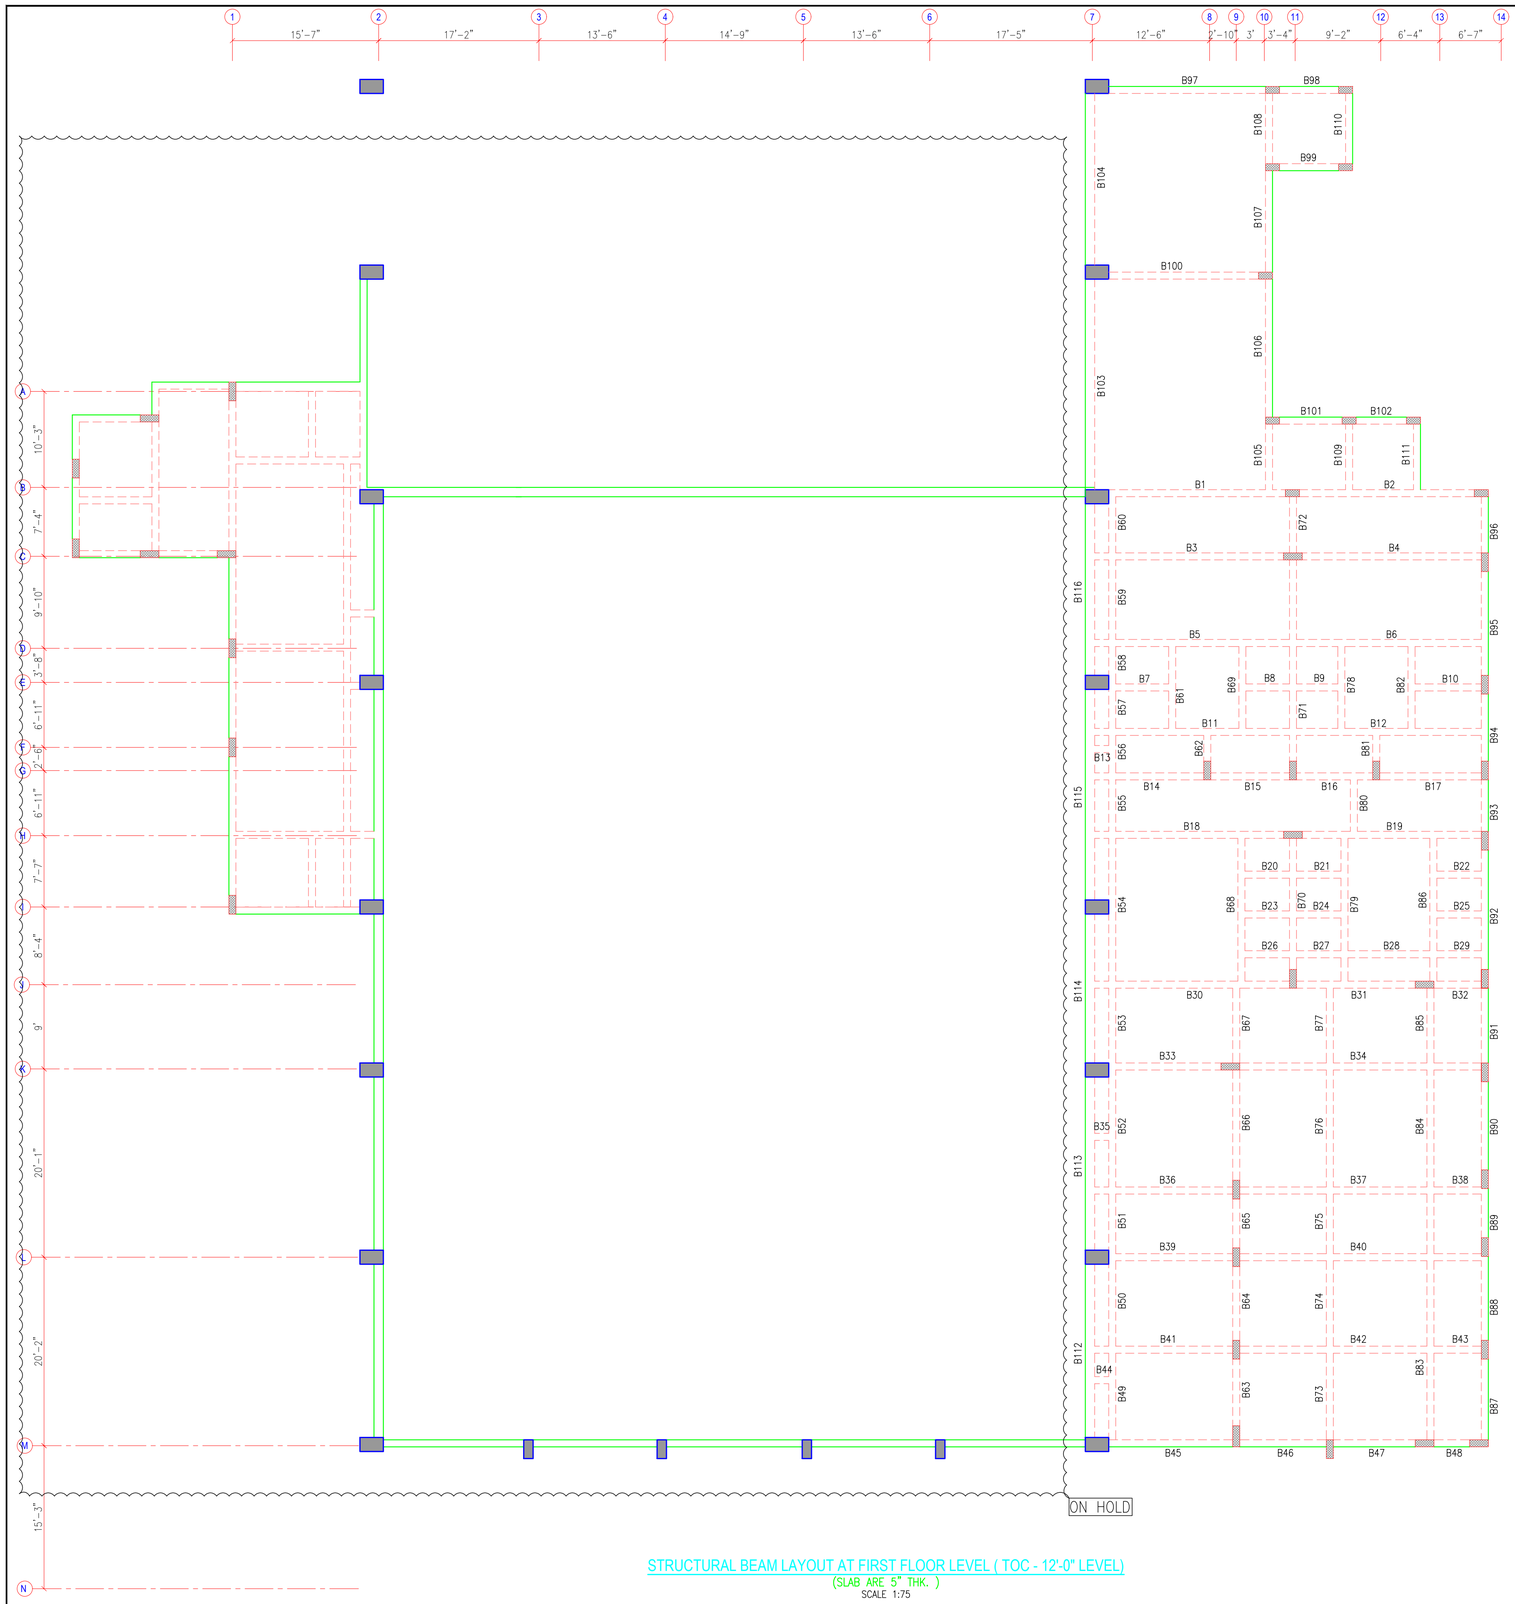

STRUCTURAL BEAM LAYOUT AT FIRST FLOOR LEVEL (TOC - 12'-0" LEVEL)
(SLAB ARE 5" THK.)
SCALE 1:75

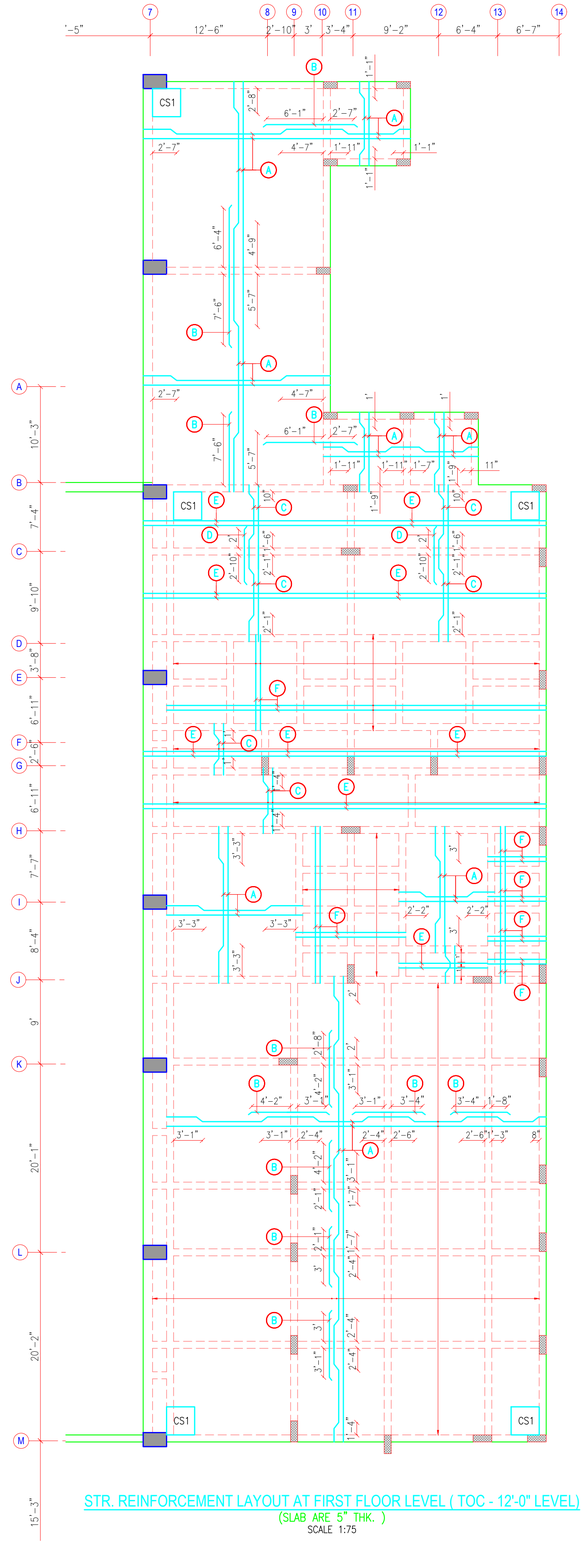

STR. REINFORCEMENT LAYOUT AT FIRST FLOOR LEVEL (TOC - 12'-0" LEVEL)
(SLAB ARE 5" THK.)
SCALE 1:75

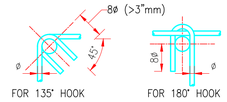

TYPICAL DETAIL OF HOOK
SCALE 1" : 2'-0"

SCHEDULE OF SLABS REINFORCEMENT

BAR MARKED	DIA	SPACING	REMARKS
A	8T	@ 150c/c	ALT-BENT UP
B	8T	@ 300c/c	EXTRA AT TOP B/W BENT UP BARS
C	8T	@ 125c/c	ALT-BENT UP
D	8T	@ 250c/c	EXTRA AT TOP B/W BENT UP BARS
E	8T	@ 200c/c	DIST. BARS AT BOTTOM
F	8T	@ 150c/c	TOP & BOTTOM JALI
CS1 – CORNER STEEL 8T@ 150 c/c TOP BOTTOM BOTHWAYS 900x900			

GENERAL NOTES FOR REINFORCED CONC. WORK

1. ALL DIMENSIONS ARE IN FOOT & INCH AND.
2. KINDLY CONFIRM THE GRID LINE DIMENSION AND COLUMN LOCATION FROM LATEST ARCHITECTURAL DRAWING.
3. CLEAR COVER
   BEAM = 30mm TO MAIN STEEL
   SLAB = 20mm TO MAIN STEEL

GRADE OF CONCRETE	GRADE OF STEEL	LAP LENGTH
M25	Fe500	46xDIA. OF BARS

ALL DIMENSIONS SHALL BE CONFIRMED AT SITE BEFORE EXECUTION OF WORK.

FOR APPROVAL

REFERENCE DRAWING

DRAWING No.	DRAWING TITLE
-	-

REVISIONS

REV	DATE	DESCRIPTION	DRN	CHK
RA	06/05/23	ISSUED FOR APPROVAL	PPS	NP

APPROVAL	NAME	DATE	APPROVAL	NAME	DATE
DESIGNER	NP	07/04/23	CLIENT	-	-
CHECKED	NP	07/04/23	PROJECT LEADER	ARS	07/04/23
DRAWN	PPS	07/04/23	DISCIPLINE	CIVIL	07/04/23

DELF CONSULTING ENGINEERS (INDIA) PVT. LTD.
101, 2nd Floor, Shanay-1, Opp. Shivalik Plaza, IIM-ATIRA Road, Ambawadi, Ahmedabad-380015, Gujarat, India
Tel : +91 79 26309993, +91 97250 05564 (M)
Fax : +91 79 26309992
Email : info@delfengineersindia.com
Web : www.delfengineersindia.com

CLIENT: RR PLUS
PROJECT: BANQUET HALL PROJECT
-
TITLE: STRUCTURAL LAYOUT AND DETAILS AT FIRST FLOOR LEVEL
SHEET 1 of 2
REV RA
SCALE U.O.N. AS SHOWN
DELF DWG No. 9248-01-T-1004
SIZE A1

FILENAME : Beam layout, slab reinforcement