THIS DRAWING IS THE PROPERTY OF DELF INDIA & SHALL NOT BE COPIED OR REPRODUCED EITHER WHOLLY OR IN PART WITHOUT THE WRITTEN PERMISSION OF THE AFORMENTIONED COMPANY

BEAM SCHEDULE (M25 : Fe500) (LEVEL: FIRST FLOOR)

BEAM NUMBERS	SIZE		BOTTOM REINFORCEMENT			TOP REINFORCEMENT			SHEAR STIRRUPS			SFR	REMARKS
	B	D	LEFT	MID SPAN	RIGHT	LEFT	MID SPAN	RIGHT	LEFT	MID SPAN	RIGHT		
B1	9"	24"	2-T16	2-T16	2-T16	2-T12	2-T12	+ 2-T12 / 2-T12	2L-T8@4" C/C	2L-T8@8" C/C	2L-T8@4" C/C	–	–
B2	9"	24"	2-T16	2-T16	2-T16	+ 2-T12 / 2-T12	2-T12	2-T12	2L-T8@4" C/C	2L-T8@8" C/C	2L-T8@4" C/C	–	–
B3	9"	24"	+ 2-T16 / 2-T12	+ 2-T16 / 2-T12	+ 2-T16 / 2-T12	2-T12	2-T12	+ 2-T12 / 2-T12	2L-T8@4" C/C	2L-T8@8" C/C	2L-T8@4" C/C	–	–
B4	9"	24"	+ 2-T16 / 2-T12	+ 2-T16 / 2-T12	+ 2-T16 / 2-T12	+ 2-T12 / 2-T12	2-T12	2-T12	2L-T8@4" C/C	2L-T8@8" C/C	2L-T8@4" C/C	–	–
B5	9"	24"	2-T16	2-T16	2-T16	2-T12	2-T12	+ 2-T12 / 2-T12	2L-T8@4" C/C	2L-T8@8" C/C	2L-T8@4" C/C	–	–
B6	9"	24"	2-T16	2-T16	2-T16	+ 2-T12 / 2-T12	2-T12	2-T12	2L-T8@4" C/C	2L-T8@8" C/C	2L-T8@4" C/C	–	–
B7	9"	24"	2-T16	2-T16	2-T16	2-T12	2-T12	2-T12	2L-T8@4" C/C	2L-T8@4" C/C	2L-T8@4" C/C	–	–
B8	9"	24"	2-T16	2-T16	2-T16	2-T12	2-T12	2-T12	2L-T8@4" C/C	2L-T8@4" C/C	2L-T8@4" C/C	–	–
B9	9"	24"	2-T16	2-T16	2-T16	2-T12	2-T12	2-T12	2L-T8@4" C/C	2L-T8@4" C/C	2L-T8@4" C/C	–	–
B10	9"	24"	2-T16	2-T16	2-T16	2-T12	2-T12	+ 2-T12 / 2-T16	2L-T8@4" C/C	2L-T8@4" C/C	2L-T8@4" C/C	–	–
B11	9"	24"	2-T16	2-T16	2-T16	2-T12	2-T12	+ 2-T12 / 2-T12	2L-T8@4" C/C	2L-T8@8" C/C	2L-T8@4" C/C	–	–
B12	9"	24"	2-T16	2-T16	2-T16	+ 2-T12 / 2-T12	2-T12	2-T12	2L-T8@4" C/C	2L-T8@8" C/C	2L-T8@4" C/C	–	–
B13	9"	24"	2-T12	2-T12	2-T12	2-T12	2-T12	2-T12	2L-T8@4" C/C	2L-T8@4" C/C	2L-T8@4" C/C	–	–
B14	9"	24"	2-T16	2-T16	2-T16	2-T12	2-T12	+ 2-T12 / 2-T16	2L-T8@4" C/C	2L-T8@4" C/C	2L-T8@4" C/C	–	–
B15	9"	24"	2-T16	2-T16	2-T16	+ 2-T12 / 2-T16	2-T12	+ 2-T12 / 2-T16	2L-T8@4" C/C	2L-T8@4" C/C	2L-T8@4" C/C	–	–
B16	9"	24"	2-T16	2-T16	2-T16	+ 2-T12 / 2-T16	2-T12	2-T12	2L-T8@4" C/C	2L-T8@4" C/C	2L-T8@4" C/C	–	–
B17	9"	24"	2-T16	2-T16	2-T16	2-T12	2-T12	+ 2-T12 / 2-T16	2L-T8@4" C/C	2L-T8@4" C/C	2L-T8@4" C/C	–	–
B18	9"	24"	+ 2-T16 / 2-T12	+ 2-T16 / 2-T12	+ 2-T16 / 2-T12	+ 2-T12 / 2-T12	2-T12	+ 2-T12 / 2-T12	2L-T8@4" C/C	2L-T8@8" C/C	2L-T8@4" C/C	–	–
B19	9"	24"	+ 2-T16 / 2-T12	+ 2-T16 / 2-T12	+ 2-T16 / 2-T12	+ 2-T12 / 2-T12	2-T12	+ 2-T12 / 2-T12	2L-T8@4" C/C	2L-T8@8" C/C	2L-T8@4" C/C	–	–
B20	9"	24"	2-T16	2-T16	2-T16	+ 2-T12 / 2-T12	2-T12	2-T12	2L-T8@4" C/C	2L-T8@4" C/C	2L-T8@4" C/C	–	–
B21	9"	24"	2-T16	2-T16	2-T16	2-T12	2-T12	+ 2-T12 / 2-T12	2L-T8@4" C/C	2L-T8@4" C/C	2L-T8@4" C/C	–	–
B22	9"	24"	2-T16	2-T16	2-T16	2-T12	2-T12	2-T12	2L-T8@4" C/C	2L-T8@4" C/C	2L-T8@4" C/C	–	–
B23	9"	24"	2-T16	2-T16	2-T16	2-T12	2-T12	+ 2-T12 / 2-T12	2L-T8@4" C/C	2L-T8@4" C/C	2L-T8@4" C/C	–	–
B24	9"	24"	2-T16	2-T16	2-T16	+ 2-T12 / 2-T12	2-T12	2-T12	2L-T8@4" C/C	2L-T8@4" C/C	2L-T8@4" C/C	–	–
B25	9"	24"	2-T16	2-T16	2-T16	2-T12	2-T12	2-T12	2L-T8@4" C/C	2L-T8@4" C/C	2L-T8@4" C/C	–	–
B26	9"	24"	2-T16	2-T16	2-T16	+ 2-T12 / 2-T12	2-T12	+ 2-T12 / 2-T12	2L-T8@4" C/C	2L-T8@4" C/C	2L-T8@4" C/C	–	–
B27	9"	24"	2-T16	2-T16	2-T16	+ 2-T12 / 2-T12	2-T12	+ 2-T12 / 2-T12	2L-T8@4" C/C	2L-T8@4" C/C	2L-T8@4" C/C	–	–
B28	9"	24"	2-T16	2-T16	2-T16	+ 2-T12 / 2-T12	2-T12	+ 2-T12 / 2-T12	2L-T8@4" C/C	2L-T8@4" C/C	2L-T8@4" C/C	–	–
B29	9"	24"	2-T16	2-T16	2-T16	+ 2-T12 / 2-T12	2-T12	+ 2-T12 / 2-T12	2L-T8@4" C/C	2L-T8@4" C/C	2L-T8@4" C/C	–	–
B30	9"	24"	+ 2-T16 / 2-T16	+ 2-T16 / 2-T16	+ 2-T16 / 2-T16	+ 2-T12 / 2-T12	2-T12	+ 2-T12 / 2-T16	2L-T8@8" C/C	2L-T8@4" C/C	2L-T8@4" C/C	–	–
B31	9"	24"	+ 2-T16 / 2-T16	+ 2-T16 / 2-T16	+ 2-T16 / 2-T16	+ 2-T12 / 2-T16	2-T12	+ 2-T12 / 2-T12	2L-T8@4" C/C	2L-T8@8" C/C	2L-T8@4" C/C	–	–
B32	9"	24"	2-T16	2-T16	2-T16	+ 2-T12 / 2-T12	2-T12	+ 2-T12 / 2-T12	2L-T8@4" C/C	2L-T8@4" C/C	2L-T8@4" C/C	–	–
B33	9"	24"	+ 2-T16 / 2-T16	+ 2-T16 / 2-T16	+ 2-T16 / 2-T16	2-T12	2-T12	+ 2-T12 / 2-T12	2L-T8@4" C/C	2L-T8@4" C/C	2L-T8@4" C/C	–	–
B34	9"	24"	+ 2-T16 / 2-T16	+ 2-T16 / 2-T16	+ 2-T16 / 2-T16	+ 2-T12 / 2-T12	+ 2-T12 / 2-T12	+ 2-T12 / 2-T12	2L-T8@4" C/C	2L-T8@4" C/C	2L-T8@4" C/C	–	–
B35	9"	24"	2-T12	2-T12	2-T12	2-T12	2-T12	+ 2-T12 / 2-T12	2L-T8@4" C/C	2L-T8@4" C/C	2L-T8@4" C/C	–	–
B36	9"	24"	+ 2-T16 / 2-T12	+ 2-T16 / 2-T12	+ 2-T16 / 2-T12	2-T12	2-T12	+ 2-T12 / 2-T16	2L-T8@8" C/C	2L-T8@4" C/C	2L-T8@4" C/C	–	–
B37	9"	24"	+ 2-T16 / 2-T12	+ 2-T16 / 2-T12	+ 2-T16 / 2-T12	+ 2-T12 / 2-T16	2-T12	+ 2-T12 / 2-T12	2L-T8@4" C/C	2L-T8@8" C/C	2L-T8@4" C/C	–	–
B38	9"	24"	2-T16	2-T16	2-T16	+ 2-T12 / 2-T12	2-T12	2-T12	2L-T8@4" C/C	2L-T8@4" C/C	2L-T8@4" C/C	–	–
B39	9"	24"	2-T20	2-T20	2-T20	2-T12	2-T12	+ 2-T12 / 2-T16	2L-T8@4" C/C	2L-T8@8" C/C	2L-T8@4" C/C	–	–
B40	9"	24"	2-T20	2-T20	2-T20	+ 2-T12 / 2-T16	2-T12	2-T12	2L-T8@4" C/C	2L-T8@8" C/C	2L-T8@4" C/C	–	–
B41	9"	24"	2-T16	2-T16	2-T16	+ 2-T12 / 2-T12	+ 2-T12 / 2-T12	+ 2-T12 / 2-T12	2L-T8@4" C/C	2L-T8@8" C/C	2L-T8@4" C/C	–	–
B42	9"	24"	2-T20	2-T20	2-T20	+ 2-T12 / 2-T12	2-T12	+ 2-T12 / 2-T12	2L-T8@4" C/C	2L-T8@8" C/C	2L-T8@4" C/C	–	–
B43	9"	24"	2-T20	2-T20	2-T20	+ 2-T12 / 2-T12	2-T12	+ 2-T12 / 2-T12	2L-T8@4" C/C	2L-T8@8" C/C	2L-T8@4" C/C	–	–
B44	9"	24"	2-T16	2-T16	2-T16	2-T12	2-T12	2-T12	2L-T8@4" C/C	2L-T8@4" C/C	2L-T8@4" C/C	–	–
B45	9"	24"	2-T16	2-T16	2-T16	2-T12	2-T12	+ 2-T12 / 2-T12	2L-T8@4" C/C	2L-T8@4" C/C	2L-T8@4" C/C	–	–
B46	9"	24"	2-T16	2-T16	2-T16	+ 2-T12 / 2-T12	2-T12	+ 2-T12 / 2-T12	2L-T8@4" C/C	2L-T8@4" C/C	2L-T8@4" C/C	–	–
B47	9"	24"	2-T16	2-T16	2-T16	+ 2-T12 / 2-T12	2-T12	+ 2-T12 / 2-T12	2L-T8@4" C/C	2L-T8@4" C/C	2L-T8@4" C/C	–	–
B48	9"	24"	2-T16	2-T16	2-T16	+ 2-T12 / 2-T12	2-T12	2-T12	2L-T8@4" C/C	2L-T8@4" C/C	2L-T8@4" C/C	–	–
B49	9"	24"	2-T16	2-T16	2-T16	2-T12	2-T12	+ 2-T12 / 2-T12	2L-T8@4" C/C	2L-T8@8" C/C	2L-T8@4" C/C	–	–
B50	9"	24"	2-T16	2-T16	2-T16	+ 2-T12 / 2-T12	2-T12	+ 2-T12 / 2-T12	2L-T8@4" C/C	2L-T8@4" C/C	2L-T8@4" C/C	–	–
B51	9"	24"	2-T16	2-T16	2-T16	+ 2-T12 / 2-T12	2-T12	+ 2-T12 / 2-T12	2L-T8@4" C/C	2L-T8@4" C/C	2L-T8@4" C/C	–	–
B52	9"	24"	2-T16	2-T16	2-T16	+ 2-T12 / 2-T12	2-T12	+ 2-T12 / 2-T12	2L-T8@4" C/C	2L-T8@8" C/C	2L-T8@4" C/C	–	–
B53	9"	24"	2-T16	2-T16	2-T16	+ 2-T12 / 2-T12	2-T12	+ 2-T12 / 2-T12	2L-T8@4" C/C	2L-T8@4" C/C	2L-T8@4" C/C	–	–
B54	9"	24"	2-T16	2-T16	2-T16	+ 2-T12 / 2-T12	2-T12	+ 2-T12 / 2-T12	2L-T8@4" C/C	2L-T8@4" C/C	2L-T8@4" C/C	–	–
B55	9"	24"	2-T16	2-T16	2-T16	+ 2-T12 / 2-T12	2-T12	+ 2-T12 / 2-T12	2L-T8@4" C/C	2L-T8@4" C/C	2L-T8@4" C/C	–	–
B56	9"	24"	2-T16	2-T16	2-T16	+ 2-T12 / 2-T12	2-T12	+ 2-T12 / 2-T12	2L-T8@4" C/C	2L-T8@4" C/C	2L-T8@4" C/C	–	–
B57	9"	24"	2-T16	2-T16	2-T16	+ 2-T12 / 2-T12	2-T12	+ 2-T12 / 2-T12	2L-T8@4" C/C	2L-T8@4" C/C	2L-T8@4" C/C	–	–
B58	9"	24"	2-T16	2-T16	2-T16	+ 2-T12 / 2-T12	2-T12	2-T12	2L-T8@4" C/C	2L-T8@4" C/C	2L-T8@4" C/C	–	–

BEAM SCHEDULE (M25 : Fe500) (LEVEL: FIRST FLOOR)

BEAM NUMBERS	SIZE		BOTTOM REINFORCEMENT			TOP REINFORCEMENT			SHEAR STIRRUPS			SFR	REMARKS
	B	D	LEFT	MID SPAN	RIGHT	LEFT	MID SPAN	RIGHT	LEFT	MID SPAN	RIGHT		
B59	9"	24"	2-T16	2-T16	2-T16	2-T12	2-T12	+ 2-T12 / 2-T12	2L-T8@4" C/C	2L-T8@4" C/C	2L-T8@4" C/C	–	–
B60	9"	24"	2-T16	2-T16	2-T16	+ 2-T12 / 2-T12	2-T12	2-T12	2L-T8@4" C/C	2L-T8@4" C/C	2L-T8@4" C/C	–	–
B61	9"	24"	2-T16	2-T16	2-T16	2-T12	2-T12	2-T12	2L-T8@4" C/C	2L-T8@8" C/C	2L-T8@4" C/C	–	–
B62	9"	24"	2-T16	2-T16	2-T16	+ 2-T12 / 2-T12	+ 2-T12 / 2-T12	+ 2-T12 / 2-T12	2L-T8@4" C/C	2L-T8@4" C/C	2L-T8@4" C/C	–	–
B63	9"	24"	2-T16	2-T16	2-T16	2-T12	2-T12	+ 2-T12 / 2-T12	2L-T8@4" C/C	2L-T8@4" C/C	2L-T8@4" C/C	–	–
B64	9"	24"	2-T16	2-T16	2-T16	+ 2-T12 / 2-T12	2-T12	+ 2-T12 / 2-T12	2L-T8@4" C/C	2L-T8@4" C/C	2L-T8@4" C/C	–	–
B65	9"	24"	2-T16	2-T16	2-T16	+ 2-T12 / 2-T12	2-T12	+ 2-T12 / 2-T12	2L-T8@4" C/C	2L-T8@4" C/C	2L-T8@4" C/C	–	–
B66	9"	24"	2-T16	2-T16	2-T16	+ 2-T12 / 2-T12	2-T12	+ 2-T12 / 2-T12	2L-T8@4" C/C	2L-T8@8" C/C	2L-T8@4" C/C	–	–
B67	9"	24"	2-T16	2-T16	2-T16	+ 2-T12 / 2-T12	+ 2-T12 / 2-T12	+ 2-T12 / 2-T12	2L-T8@4" C/C	2L-T8@4" C/C	2L-T8@4" C/C	–	–
B68	9"	24"	+ 2-T16 / 2-T12	+ 2-T16 / 2-T12	+ 2-T16 / 2-T12	+ 2-T12 / 2-T12	+ 2-T12 / 2-T12	+ 2-T12 / 2-T12	2L-T8@4" C/C	2L-T8@8" C/C	2L-T8@4" C/C	–	–
B69	9"	24"	2-T16	2-T16	2-T16	2-T12	2-T12	2-T12	2L-T8@4" C/C	2L-T8@4" C/C	2L-T8@4" C/C	–	–
B70	9"	24"	+ 2-T20 / 2-T12	+ 2-T20 / 2-T12	+ 2-T20 / 2-T12	+ 2-T16 / 2-T12	+ 2-T16 / 2-T12	+ 2-T16 / 2-T12	2L-T8@4" C/C	2L-T8@4" C/C	2L-T8@4" C/C	–	–
B71	9"	24"	+ 2-T20 / 2-T12	+ 2-T20 / 2-T12	+ 2-T20 / 2-T12	+ 2-T16 / 2-T12	+ 2-T16 / 2-T12	+ 2-T16 / 2-T12	2L-T8@4" C/C	2L-T8@8" C/C	2L-T8@4" C/C	–	–
B72	9"	24"	+ 2-T20 / 2-T12	+ 2-T20 / 2-T12	+ 2-T20 / 2-T12	+ 2-T12 / 2-T12	+ 2-T12 / 2-T12	+ 2-T12 / 2-T12	2L-T8@4" C/C	2L-T8@4" C/C	2L-T8@4" C/C	–	–
B73	9"	24"	2-T16	2-T16	2-T16	2-T12	2-T12	+ 2-T12 / 2-T12	2L-T8@4" C/C	2L-T8@4" C/C	2L-T8@4" C/C	–	–
B74	9"	24"	2-T16	2-T16	2-T16	+ 2-T12 / 2-T12	2-T12	2-T12	2L-T8@4" C/C	2L-T8@4" C/C	2L-T8@4" C/C	–	–
B75	9"	24"	2-T16	2-T16	2-T16	2-T12	2-T12	+ 2-T12 / 2-T12	2L-T8@4" C/C	2L-T8@4" C/C	2L-T8@4" C/C	–	–
B76	9"	24"	2-T16	2-T16	2-T16	+ 2-T12 / 2-T12	2-T12	2-T12	2L-T8@4" C/C	2L-T8@4" C/C	2L-T8@4" C/C	–	–
B77	9"	24"	2-T16	2-T16	2-T16	2-T12	2-T12	+ 2-T12 / 2-T12	2L-T8@4" C/C	2L-T8@4" C/C	2L-T8@4" C/C	–	–
B78	9"	24"	2-T16	2-T16	2-T16	2-T12	2-T12	2-T12	2L-T8@4" C/C	2L-T8@4" C/C	2L-T8@4" C/C	–	–
B79	9"	24"	+ 2-T16 / 2-T12	+ 2-T16 / 2-T12	+ 2-T16 / 2-T12	+ 2-T12 / 2-T12	+ 2-T12 / 2-T12	+ 2-T12 / 2-T12	2L-T8@4" C/C	2L-T8@8" C/C	2L-T8@4" C/C	–	–
B80	9"	24"	2-T16	2-T16	2-T16	2-T12	2-T12	2-T12	2L-T8@4" C/C	2L-T8@4" C/C	2L-T8@4" C/C	–	–
B81	9"	24"	2-T16	2-T16	2-T16	+ 2-T12 / 2-T12	+ 2-T12 / 2-T12	+ 2-T12 / 2-T12	2L-T8@4" C/C	2L-T8@4" C/C	2L-T8@4" C/C	–	–
B82	9"	24"	2-T16	2-T16	2-T16	2-T12	2-T12	2-T12	2L-T8@4" C/C	2L-T8@4" C/C	2L-T8@4" C/C	–	–
B83	9"	24"	2-T16	2-T16	2-T16	2-T12	2-T12	+ 2-T12 / 2-T12	2L-T8@4" C/C	2L-T8@8" C/C	2L-T8@4" C/C	–	–
B84	9"	24"	2-T16	2-T16	2-T16	+ 2-T12 / 2-T12	2-T12	+ 2-T12 / 2-T12	2L-T8@4" C/C	2L-T8@4" C/C	2L-T8@4" C/C	–	–
B85	9"	24"	2-T16	2-T16	2-T16	+ 2-T12 / 2-T12	2-T12	+ 2-T12 / 2-T12	2L-T8@4" C/C	2L-T8@4" C/C	2L-T8@4" C/C	–	–
B86	9"	24"	+ 2-T16 / 2-T12	+ 2-T16 / 2-T12	+ 2-T16 / 2-T12	+ 2-T12 / 2-T12	+ 2-T12 / 2-T12	+ 2-T12 / 2-T12	2L-T8@4" C/C	2L-T8@8" C/C	2L-T8@4" C/C	–	–
B87	9"	24"	2-T16	2-T16	2-T16	2-T12	2-T12	+ 2-T12 / 2-T12	2L-T8@4" C/C	2L-T8@4" C/C	2L-T8@4" C/C	–	–
B88	9"	24"	2-T16	2-T16	2-T16	+ 2-T12 / 2-T12	2-T12	2-T12	2L-T8@4" C/C	2L-T8@4" C/C	2L-T8@4" C/C	–	–
B89	9"	24"	2-T16	2-T16	2-T16	2-T12	2-T12	+ 2-T12 / 2-T12	2L-T8@4" C/C	2L-T8@4" C/C	2L-T8@4" C/C	–	–
B90	9"	24"	2-T16	2-T16	2-T16	+ 2-T12 / 2-T12	2-T12	+ 2-T12 / 2-T12	2L-T8@4" C/C	2L-T8@4" C/C	2L-T8@4" C/C	–	–
B91	9"	24"	2-T16	2-T16	2-T16	+ 2-T12 / 2-T12	2-T12	+ 2-T12 / 2-T12	2L-T8@4" C/C	2L-T8@4" C/C	2L-T8@4" C/C	–	–
B92	9"	24"	2-T16	2-T16	2-T16	+ 2-T12 / 2-T12	2-T12	+ 2-T12 / 2-T12	2L-T8@4" C/C	2L-T8@4" C/C	2L-T8@4" C/C	–	–
B93	9"	24"	2-T16	2-T16	2-T16	+ 2-T12 / 2-T12	2-T12	+ 2-T12 / 2-T12	2L-T8@4" C/C	2L-T8@4" C/C	2L-T8@4" C/C	–	–
B94	9"	24"	2-T16	2-T16	2-T16	+ 2-T12 / 2-T12	2-T12	+ 2-T12 / 2-T12	2L-T8@4" C/C	2L-T8@4" C/C	2L-T8@4" C/C	–	–
B95	9"	24"	2-T16	2-T16	2-T16	+ 2-T12 / 2-T12	2-T12	+ 2-T12 / 2-T12	2L-T8@4" C/C	2L-T8@4" C/C	2L-T8@4" C/C	–	–
B96	9"	24"	2-T16	2-T16	2-T16	+ 2-T12 / 2-T12	2-T12	+ 2-T12 / 2-T12	2L-T8@4" C/C	2L-T8@4" C/C	2L-T8@4" C/C	–	–
B97	9"	24"	3-T12	3-T12	3-T12	3-T12	3-T12	3-T12	2L-T8@4" C/C	2L-T8@8" C/C	2L-T8@4" C/C	–	–
B98	9"	24"	3-T12	3-T12	3-T12	3-T12	3-T12	3-T12	2L-T8@4" C/C	2L-T8@4" C/C	2L-T8@4" C/C	–	–
B99	9"	24"	3-T12	3-T12	3-T12	3-T12	3-T12	3-T12	2L-T8@4" C/C	2L-T8@4" C/C	2L-T8@4" C/C	–	–
B100	9"	24"	3-T12	3-T12	3-T12	3-T12	3-T12	3-T12	2L-T8@4" C/C	2L-T8@8" C/C	2L-T8@4" C/C	–	–
B101	9"	24"	3-T12	3-T12	3-T12	3-T12	3-T12	3-T12	2L-T8@4" C/C	2L-T8@4" C/C	2L-T8@4" C/C	–	–
B102	9"	24"	3-T12	3-T12	3-T12	3-T12	3-T12	3-T12	2L-T8@4" C/C	2L-T8@4" C/C	2L-T8@4" C/C	–	–
B103	1'	24"	+ 3-T20 / 3-T16	3-T20	+ 3-T20 / 3-T16	3-T20	3-T20	3-T20	2L-T8@4" C/C	2L-T8@8" C/C	2L-T8@4" C/C	–	–
B104	1'	24"	+ 3-T20 / 3-T16	3-T20	+ 3-T20 / 3-T16	3-T20	3-T20	3-T20	2L-T8@4" C/C	2L-T8@8" C/C	2L-T8@4" C/C	–	–
B105	9"	24"	3-T12	3-T12	3-T12	+ 3-T12 / 2-T12	+ 3-T12 / 2-T12	+ 3-T12 / 2-T12	2L-T8@4" C/C	2L-T8@4" C/C	2L-T8@4" C/C	–	CANTILEVER
B106	9"	24"	3-T12	3-T12	3-T12	3-T12	3-T12	3-T12	2L-T8@4" C/C	2L-T8@4" C/C	2L-T8@4" C/C	–	–
B107	9"	24"	3-T12	3-T12	3-T12	3-T12	3-T12	3-T12	2L-T8@4" C/C	2L-T8@4" C/C	2L-T8@4" C/C	–	–
B108	9"	24"	3-T12	3-T12	3-T12	3-T12	3-T12	3-T12	2L-T8@4" C/C	2L-T8@4" C/C	2L-T8@4" C/C	–	–
B109	9"	24"	3-T12	3-T12	3-T12	+ 3-T12 / 2-T12	+ 3-T12 / 2-T12	+ 3-T12 / 2-T12	2L-T8@4" C/C	2L-T8@4" C/C	2L-T8@4" C/C	–	CANTILEVER
B110	9"	24"	3-T12	3-T12	3-T12	3-T12	3-T12	3-T12	2L-T8@4" C/C	2L-T8@4" C/C	2L-T8@4" C/C	–	–
B111	9"	24"	3-T12	3-T12	3-T12	+ 3-T12 / 2-T12	+ 3-T12 / 2-T12	+ 3-T12 / 2-T12	2L-T8@4" C/C	2L-T8@4" C/C	2L-T8@4" C/C	–	CANTILEVER
B112	1'	24"	3-T20	3-T20	3-T20	3-T20	3-T20	3-T20	2L-T8@4" C/C	2L-T8@8" C/C	2L-T8@4" C/C	–	CANTILEVER
B113	1'	24"	3-T20	3-T20	+ 3-T20 / 3-T16	3-T20	3-T20	3-T20	2L-T8@4" C/C	2L-T8@8" C/C	2L-T8@4" C/C	–	–
B114	1'	24"	+ 3-T20 / 3-T16	3-T20	+ 3-T20 / 3-T16	3-T20	3-T20	3-T20	2L-T8@4" C/C	2L-T8@8" C/C	2L-T8@4" C/C	–	–
B115	1'	24"	+ 3-T20 / 3-T16	3-T20	+ 3-T20 / 3-T16	3-T20	3-T20	3-T20	2L-T8@4" C/C	2L-T8@8" C/C	2L-T8@4" C/C	–	–
B116	1'	24"	+ 3-T20 / 3-T16	3-T20	+ 3-T20 / 3-T16	3-T20	3-T20	3-T20	2L-T8@4" C/C	2L-T8@8" C/C	2L-T8@4" C/C	–	–

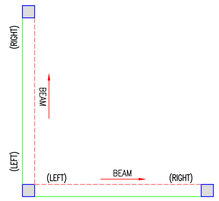

BEAM SCHEDULE READING LAYOUT

SCALE 1:50

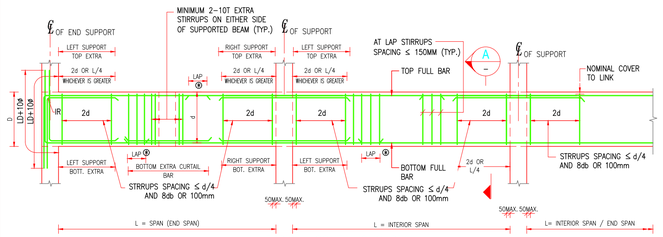

TYPICAL CONTINUOUS BEAM

SCALE 1:20

⊕ LAP LENGTH SHALL NOT BE LESS THAN Ld
Ld= DEVELOPMENT LENGTH OF LARGEST LONGITUDINAL BAR

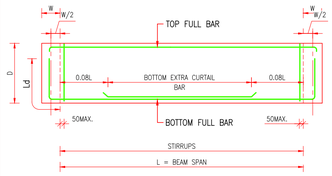

TYPICAL SIMPLY SUPPORTED SECONDARY BEAM

SCALE 1:20

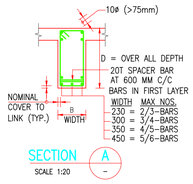

SECTION A

SCALE 1:20

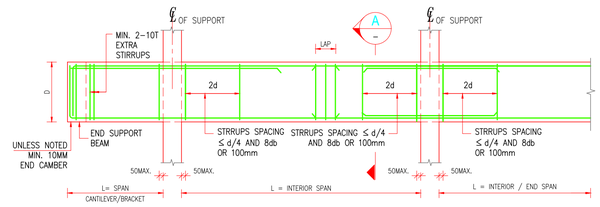

TYPICAL CONTINUOUS BEAM WITH BRACKET

SCALE 1:20

REFERENCE DRAWING

DRAWING No.	DRAWING TITLE
-	-

REVISIONS

REV	DATE	DESCRIPTION	DRN	CHK
RA	06/05/23	ISSUED FOR APPROVAL	PPS	NP

APPROVAL	NAME	DATE	APPROVAL	NAME	DATE
DESIGNER	NP	07/04/23	CLIENT	-	-
CHECKED	NP	07/04/23	PROJECT LEADER	ARS	07/04/23
DRAWN	PPS	07/04/23	DISCIPLINE	CIVIL	07/04/23

DELF CONSULTING ENGINEERS (INDIA) PVT. LTD.
101, 2nd Floor, Shanay-1, Opp. Shivalik Plaza, IIM-ATIRA Road, Ambawadi, Ahmedabad-380015, Gujarat, India
Tel : +91 79 26309993, +91 97250 05564 (M)
Fax : +91 79 26309992
Email : info@delfengineersindia.com
Web : www.delfengineersindia.com

CLIENT: RR PLUS

PROJECT: BANQUET HALL PROJECT

-

TITLE: BEAM SCHEDULE AT FIRST FLOOR LEVEL

SHEET 2 of 2

SCALE U.O.N. AS SHOWN

DELF DWG No. 9248-01-T-1004

SIZE A1

REV RA

FILENAME : Beam layout, slab reinforcement