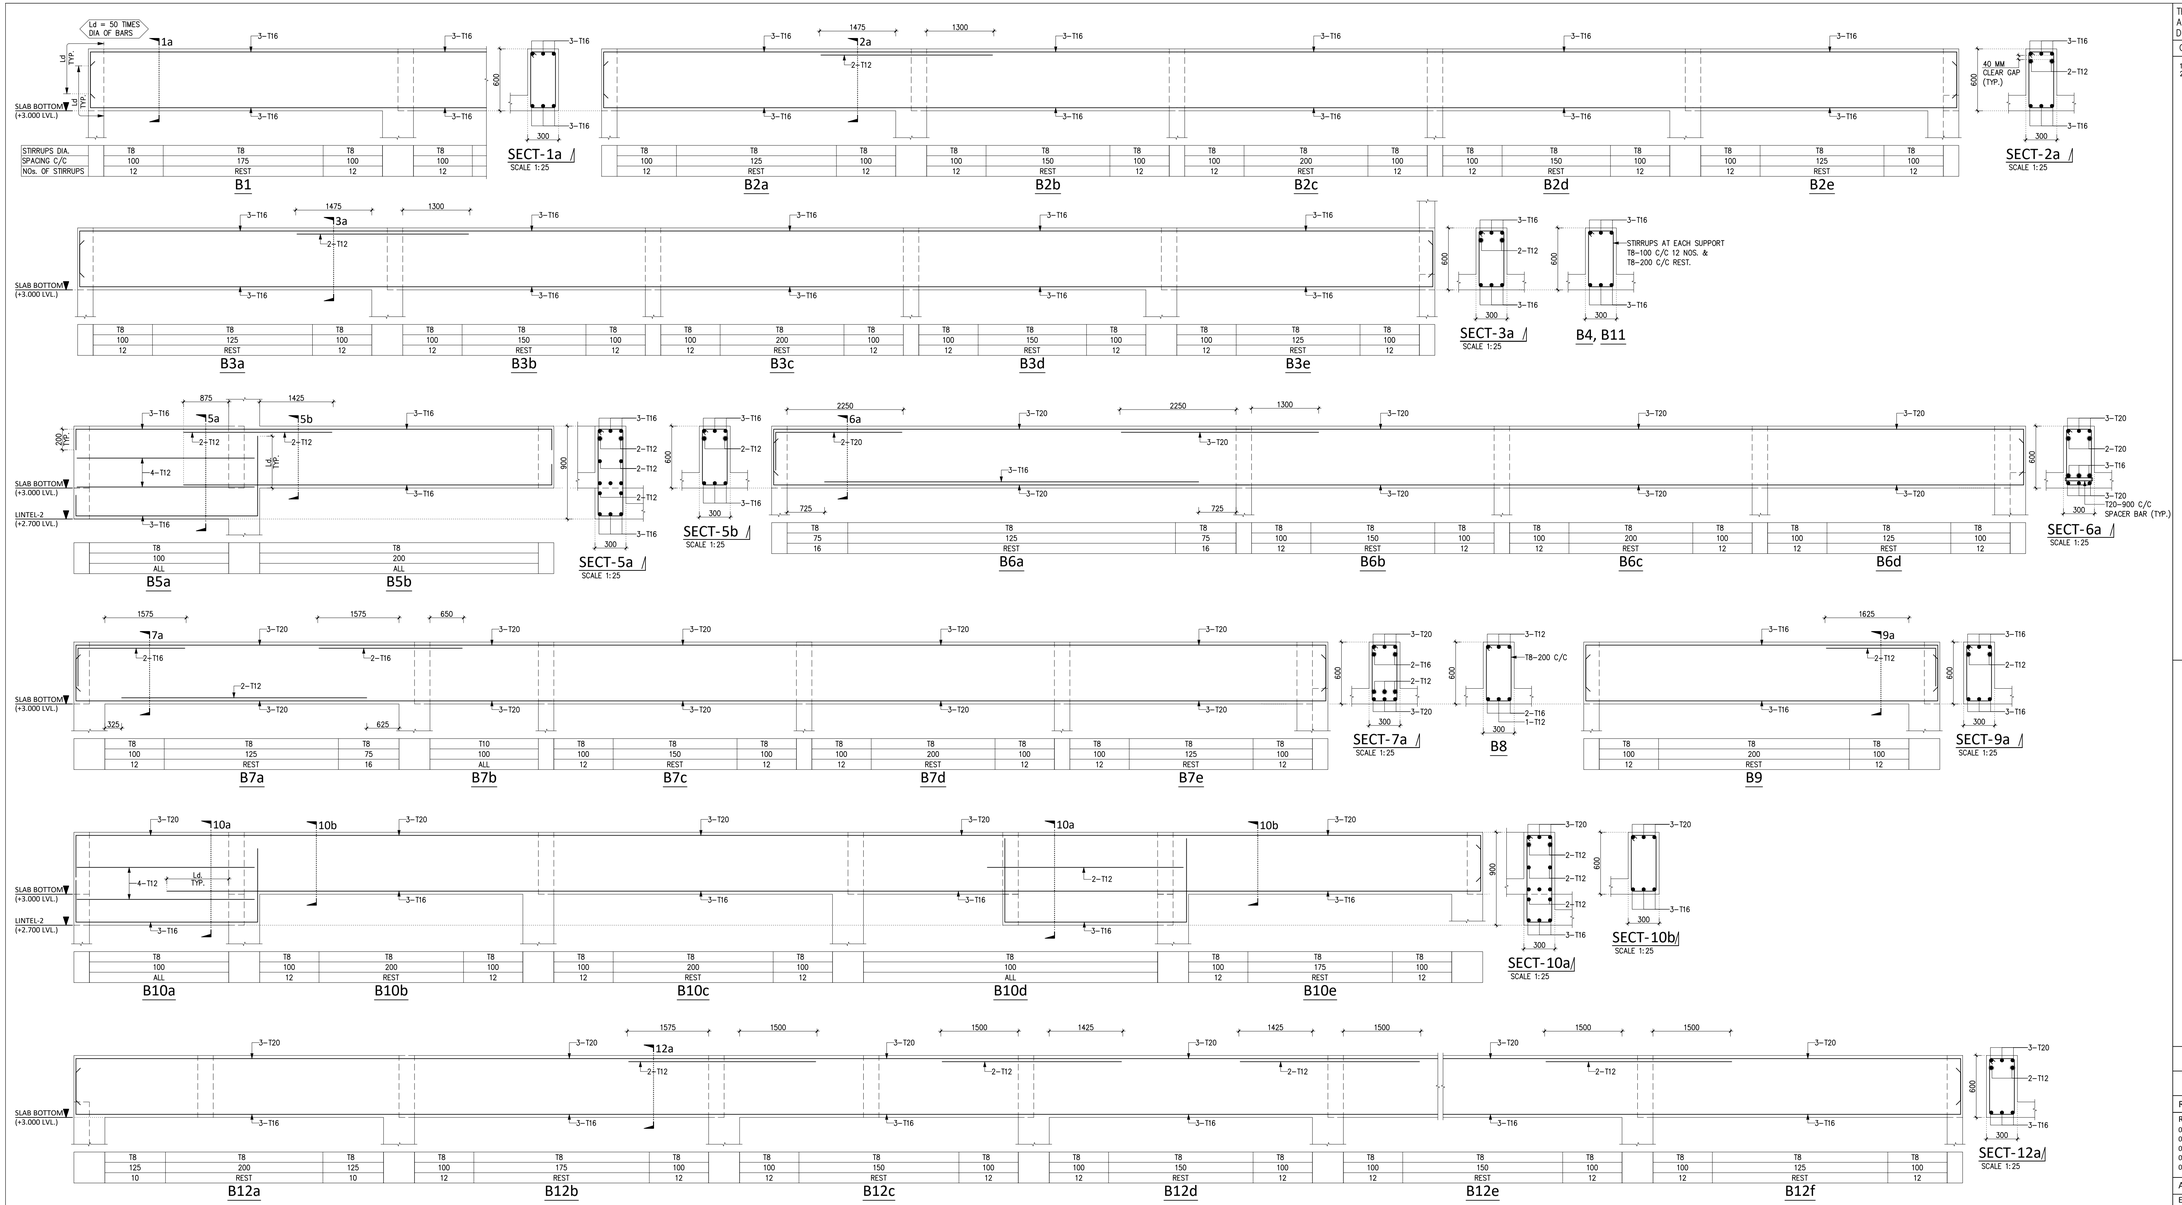

STIRRUPS DIA.	T8	T8	T8		T8
SPACING C/C	100	175	100		100
NOs. OF STIRRUPS	12	REST	12		12

B1

T8	T8	T8		T8	T8	T8		T8	T8	T8		T8	T8	T8
100	125	100		100	150	100		100	200	100		100	125	100
12	REST	12		12	REST	12		12	REST	12		12	REST	12

B2a B2b B2c B2d B2e

T8	T8	T8	T8	T8	T8	T8	T8	T8	T8	T8	T8	T8	T8	T8
100	125	100	100	150	100	100	200	100	100	150	100	100	125	100
12	REST	12	12	REST	12	12	REST	12	12	REST	12	12	REST	12

B3a B3b B3c B3d B3e

B4, B11

T8	T8		T8	T8
100	200		100	200
ALL	ALL		ALL	ALL

B5a B5b

T8	T8	T8		T8	T8	T8		T8	T8	T8		T8	T8	T8
75	125	75		100	150	100		100	200	100		100	125	100
16	REST	16		12	REST	12		12	REST	12		12	REST	12

B6a B6b B6c B6d

T8	T8	T8	T10	T8	T8	T8	T8	T8	T8	T8	T8	T8	T8	T8	T8	T8	T8	T8
100	125	75	100	100	150	100	100	200	100	100	125	100	100	125	100	100	125	100
12	REST	16	ALL	12	REST	12	12	REST	12	12	REST	12	12	REST	12	12	REST	12

B7a B7b B7c B7d B7e

B8

T8	T8	T8
100	200	100
12	REST	12

B9

T8	T8	T8		T8	T8	T8		T8	T8	T8		T8	T8	T8		T8	T8	T8
125	200	125		100	175	100		100	150	100		100	150	100		100	125	100
10	REST	10		12	REST	12		12	REST	12		12	REST	12		12	REST	12

B12a B12b B12c B12d B12e B12f

THIS DRAWING IS EXCLUSIVE PROPERTY OF "S3M DESIGN CONSULTANTS LL
AND SHOULD NOT BE USED,COPIED,REPRODUCED AND EXHIBITED IN ANY W
DETRIMENTAL TO OUR INTEREST WITHOUT OUR WRITTEN CONSENT.

GENERAL NOTES :

1. ALL DIMENSIONS ARE IN mm. & LEVELS ARE IN METER.
2. FOR ALL OTHER NOTES & DETAILS REFER DRAWING NO. 02.SR.06.

REV NO.	DESCRIPTION	DATE	DRAWN	CHECKED
R2	REVISED AS PER ARCH. DRAWING	27-02-19	ROHIT	ROSHAN
R1	REVISED AS PER ARCH. DRAWING	22-02-19	ROHIT	ROSHAN

REF. DRGS. :
01. ARCHITECTURAL : -----
02. STRUCTURAL : 02.SR.06
03. HVAC : -----
04. ELECTRICAL : -----
05. UTILITIES : -----

ASSOCIATES :

ELECTRICAL ---	FIRE SAFETY ---
MECH. UTILITIES ---	HVAC ---

STRU. DETAILS AT SLAB-1 BOTTOM (+3.000) &
SLAB-2 BOTTOM (+4.500) LVL.

KITCHEN BLOCK

SECONDARY PAEDIATRIC CARE CENTER

TORNASCENT CARE INSTITUTE , SURAT

PROJECT NO:	DRAWING NUMBER :		REVISION
1837	02.SR.07		R2
DRAWN	ROHIT	SCALE 1:25	CONSTRUCTION C
DESIGNED	ROSHAN		
CHECKED	RUTUL	DATE : 20-02-2019	600x1000
APPROVED	R.H.S.		

S3M DESIGN CONSULTANTS LLP
ENGINEERING + PLANNING
B-801, WESTGATE, NEAR YMCA CLUB, S G HIGHWAY, AHMEDABAD-
PHONE: +91 (079) 66118122/66118123
W: www.s3mconsultants.com E: s3m@s3mconsultants.com