This drawing is the property of Larsen & Toubro Limited , EDRC – B&F OC and must not be passed on to any person or body not authorised by us to receive it nor be copied or otherwise made use either in full or in part by such person or body without our prior permission in writing

+0.000M LVL CORRESPONDS TO +50.250M RL

WALL ID W10 NOT IN USE

FOR FLOOR BEAM DETAILS REFER CORRESPONDING DRAWINGS

FOR SLAB PROJECTION DETAILS REFER RESPECTIVE FLOOR NUMERATION DRGS

FOR GROOVE DETAILS REFER ARCHITECTURAL ELEVATION DRAWINGS

B – INDICATES WALL POSITION IS MIRROR

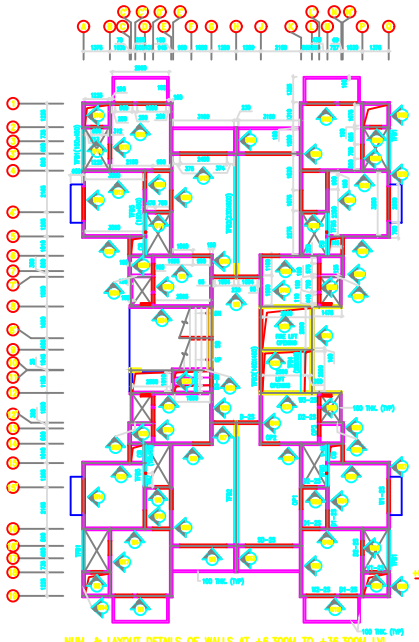

NUM. & LAYOUT DETAILS OF WALLS AT +6.300M TO +36.300M LVL
(WALL THICKNESS SHALL BE 150 THK. UNLESS OTHERWISE SPECIFIED)

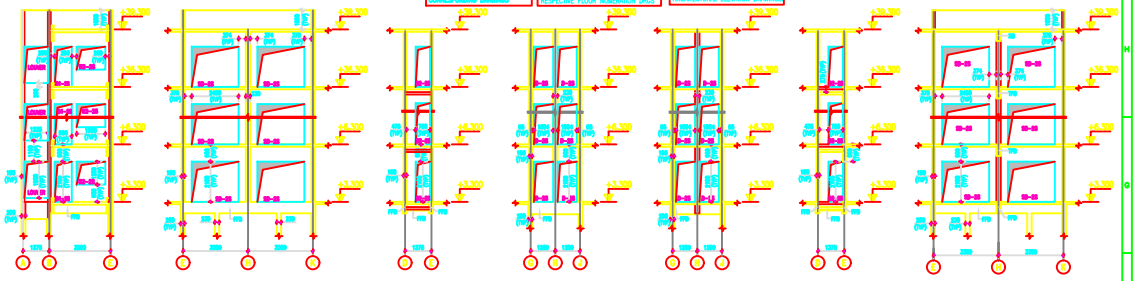

ELEVATION OF WALL W1 ALONG GRID (1)
ELEVATION OF WALL W3 ALONG GRID (10)
ELEVATION OF WALL W5 ALONG GRID (5) (W6 SHALL BE MIRROR IMAGE OF W5)
ELEVATION OF WALL W7 ALONG GRID (7)
ELEVATION OF WALL W8 ALONG GRID (7)
ELEVATION OF WALL W11 ALONG GRID (4) (W12 SHALL BE MIRROR IMAGE OF W11)
ELEVATION OF WALL W13 ALONG GRID (3)

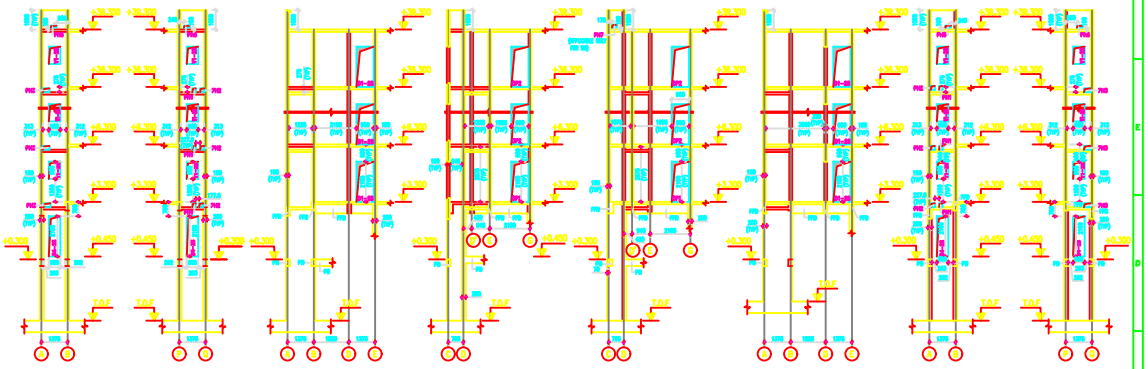

ELEVATION OF WALL W2 ALONG GRID (1)
ELEVATION OF WALL W2M ALONG GRID (10)
ELEVATION OF WALL W4 ALONG GRID (5) (W6 SHALL BE MIRROR IMAGE OF W4)
ELEVATION OF WALL W6 ALONG GRID (5) (W7 SHALL BE MIRROR IMAGE OF W6)
ELEVATION OF WALL W9 ALONG GRID (4) (W12 SHALL BE MIRROR IMAGE OF W9)
ELEVATION OF WALL W12 ALONG GRID (4)
ELEVATION OF WALL W14 ALONG GRID (3)
ELEVATION OF WALL W14M ALONG GRID (3) (W13 SHALL BE MIRROR IMAGE OF W14)

ELEVATION OF WALL W36

ELEVATION OF WALL W2SM

SCHEDULE OF PHE OPENING:–

OPENING ID	SIZE OF OPENING (W XH)
PH1	175x200
PH2	210x200
PH3	300x200
PH4	100x100
PH5	300x100
PH6	200x100
PH7	225x150
PH8	150x150
PH9	400x150

LEGEND:

- TFB – TYPICAL FLOOR BEAM
- TOF – TOP OF FOOTING
- FGL – FORMED GROUND LEVEL
- PB – PLINTH BEAM
- FFB – FIRST FLOOR BEAM
- RB – ROOF BEAM
- – 150THK. RC WALL
- – 160THK. RC WALL
- – 230THK. RC WALL

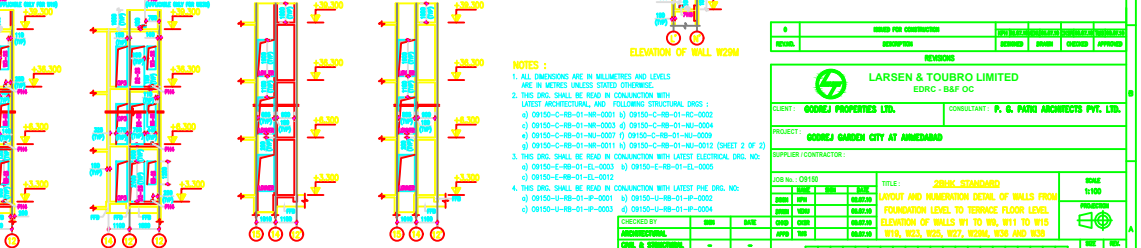

ELEVATION OF WALL W15 ALONG GRID (1) (W16 SHALL BE MIRROR IMAGE OF W15)
ELEVATION OF WALL W27 ALONG GRID (1) (W28 SHALL BE MIRROR IMAGE OF W27)
ELEVATION OF WALL W19 ALONG GRID (1) (W20 SHALL BE MIRROR IMAGE OF W19)
ELEVATION OF WALL W23 ALONG GRID (1) (W24 SHALL BE MIRROR IMAGE OF W23)
ELEVATION OF WALL W25 ALONG GRID (1) (W26 SHALL BE MIRROR IMAGE OF W25)
ELEVATION OF WALL W38 ALONG GRID (1) (W39 SHALL BE MIRROR IMAGE OF W38)

NOTES :

1. ALL DIMENSIONS ARE IN MILLIMETRES AND LEVELS ARE IN METRES UNLESS STATED OTHERWISE.
2. THIS DRG. SHALL BE READ IN CONJUNCTION WITH LATEST ARCHITECTURAL AND FOLLOWING STRUCTURAL DRGS :
   a) 09150–C–RB–01–NR–0001 b) 09150–C–RB–01–RC–0002
   c) 09150–C–RB–01–NR–0003 d) 09150–C–RB–01–NU–0004
   e) 09150–C–RB–01–NU–0007 f) 09150–C–RB–01–NU–0009
   g) 09150–C–RB–01–NR–0011 h) 09150–C–RB–01–NU–0012 (SHEET 2 OF 2)
3. THIS DRG. SHALL BE READ IN CONJUNCTION WITH LATEST ELECTRICAL DRG. NO:
   a) 09150–E–RB–01–EL–0003 b) 09150–E–RB–01–EL–0005
   c) 09150–E–RB–01–EL–0012
4. THIS DRG. SHALL BE READ IN CONJUNCTION WITH LATEST PHE DRG. NO:
   a) 09150–U–RB–01–IP–0001 b) 09150–U–RB–01–IP–0002
   c) 09150–U–RB–01–IP–0003 d) 09150–U–RB–01–IP–0004

CHECKED BY	SIGN	DATE
ARCHITECTURAL		
CIVIL & STRUCTURAL	"	"
PUBLIC HEALTH ENGG.		
HVAC	"	"
ELECTRICAL		
FIRE ENGINEERING		

REVISIONS					
0	ISSUED FOR CONSTRUCTION	DD MMM YYYY	DD MMM YYYY	DD MMM YYYY	DD MMM YYYY
REVISION	DESCRIPTION	REVISED	DRAWN	CHECKED	APPROVED

LARSEN & TOUBRO LIMITED
EDRC - B&F OC

CLIENT : GODREJ PROPERTIES LTD.
CONSULTANT : P. G. PATEL ARCHITECTS PVT. LTD.
PROJECT : GODREJ GARDEN CITY AT AHMEDABAD
SUPPLIER / CONTRACTOR :

JOB No. : C9150

	NAME	SIGN	DATE
DRAWN	GPM		03.07.10
DESIGN	VDKV		03.07.10
CHKD	CCES		03.07.10
APPD	TMS		03.07.10

TITLE : 2BHK STANDARD
LAYOUT AND NUMERATION DETAIL OF WALLS FROM FOUNDATION LEVEL TO TERRACE FLOOR LEVEL
ELEVATION OF WALLS W1 TO W9, W11 TO W15 W19, W23, W25, W27, W2MM, W36 AND W38

SCALE 1:100
PROJECTION

DRG. No. 0 9 1 5 0 – C – R B – 0 1 – N U – 0 0 1 2
SHEET 1 OF 2
SIZE A1
REV. 0

SCHEDULED FOR: ☐ PRELIMINARY ☐ TENDER ☐ INFORMATION ☐ APPROVAL ☑ CONSTRUCTION