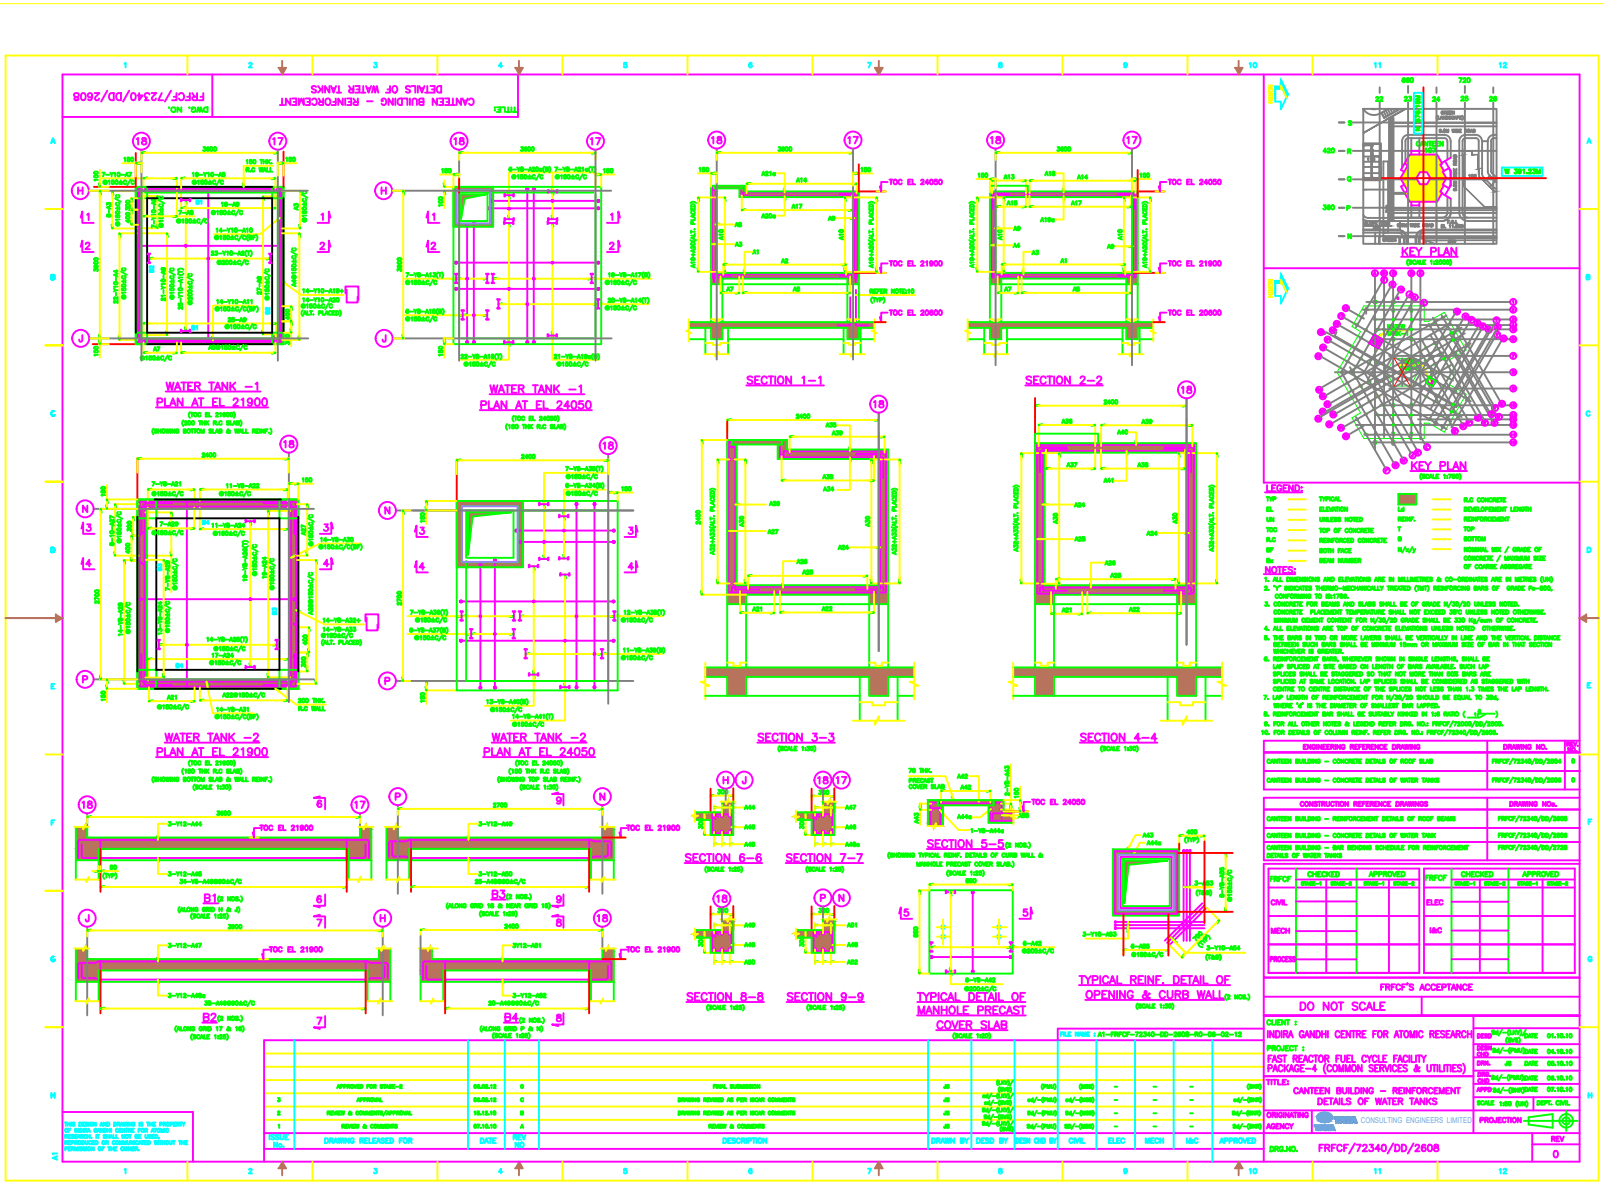
WATER TANK –1
PLAN AT EL 21900
WATER TANK –1
PLAN AT EL 24050
SECTION 1–1
SECTION 2–2
WATER TANK –2
PLAN AT EL 21900
WATER TANK –2
PLAN AT EL 24050
SECTION 3–3
SECTION 4–4
SECTION 6–6
SECTION 7–7
SECTION 5–5
SECTION 8–8
SECTION 9–9
TYPICAL DETAIL OF MANHOLE PRECAST COVER SLAB
TYPICAL REINF. DETAIL OF OPENING & CURB WALL
KEY PLAN
KEY PLAN
LEGEND:
NOTES:
ENGINEERING REFERENCE DRAWING
CONSTRUCTION REFERENCE DRAWINGS
DO NOT SCALE
FRFCF'S ACCEPTANCE
CLIENT : INDIRA GANDHI CENTRE FOR ATOMIC RESEARCH
PROJECT : FAST REACTOR FUEL CYCLE FACILITY PACKAGE-4 (COMMON SERVICES & UTILITIES)
TITLE: CANTEEN BUILDING – REINFORCEMENT DETAILS OF WATER TANKS
ORIGINATING AGENCY CONSULTING ENGINEERS LIMITED
PROJECTION
DRG.NO. FRFCF/72340/DD/2608
REV 0
DRAWN BY
DESD BY
DESN CKD BY
CIVIL
ELEC
MECH
I&C
APPROVED
DRAWING RELEASED FOR
DATE
DESCRIPTION
FINAL SUBMISSION
DRAWING REVISED AS PER NGCR COMMENTS
REVIEW & COMMENTS
APPROVAL
REVIEW & COMMENTS/APPROVAL
APPROVED FOR STAGE-2
THIS DESIGN AND DRAWING IS THE PROPERTY OF INDIRA GANDHI CENTRE FOR ATOMIC RESEARCH. IT SHALL NOT BE LENT, REPRODUCED OR COMMUNICATED WITHOUT THE PERMISSION OF THE OWNER.
TITLE: CANTEEN BUILDING – REINFORCEMENT DETAILS OF WATER TANKS
DWG. NO. FRFCF/72340/DD/2608